C. HARWELL
1413 Clifton Lane
Nashville , TN 37215

New Residence

C. HARWELL
1413 Clifton Lane
Nashville , TN 37215

SHEET INDEX

ID	Name
T1	TITLE SHEET
C1	SITE PLAN
A1	FLOOR PLANS
A2	FND & ROOF PLNS
A3	ELEVATIONS
A4	SECTIONS
A5	GARAGE PLANS
A6	GARAGE ELEVATIONs, SECT...

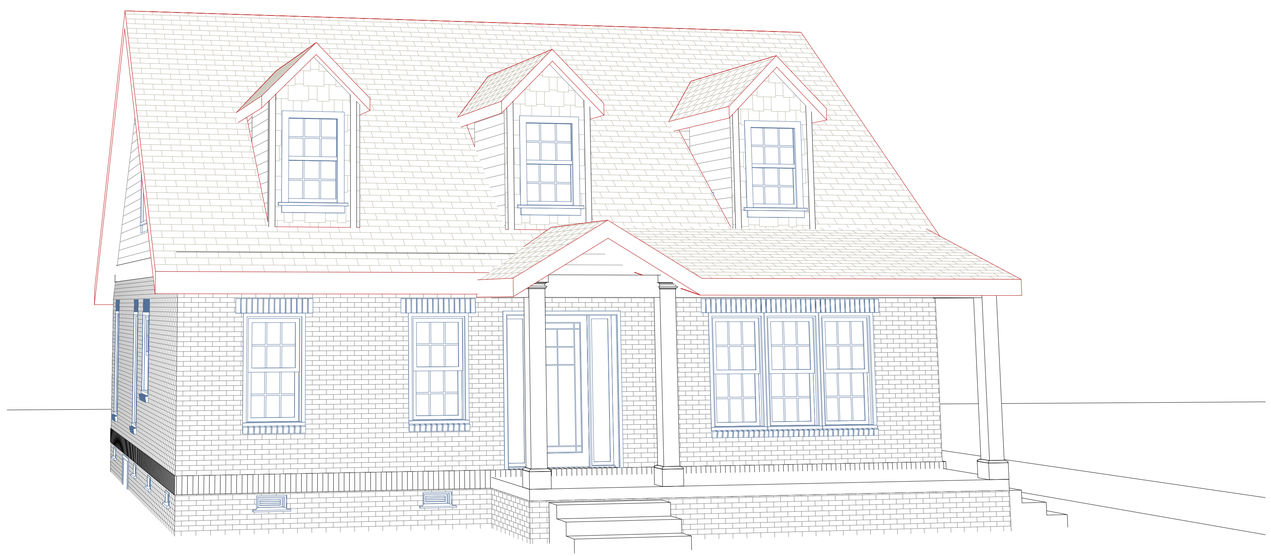

6/6/23

QUIRK DESIGNS
2331 BERRY HILL DRIVE
SUITE 203
NASHVILLE, TN 37204
Phone: (615) 269-9248 Fax: (615) 627-1298
email: quirkdesigns@comcast.net

New Residence
C. HARWELL
1413 Clifton Lane
Nashville , TN 37215

DATE: 6/6/23
REVISION

PROJECT NO: 15-110

COPYRIGHT 6/6/23
QUIRK DESIGNS

TITLE SHEET

T1
SHEET 1

C. HARWELL
1413 Clifton Lane
Nashville , TN 37215

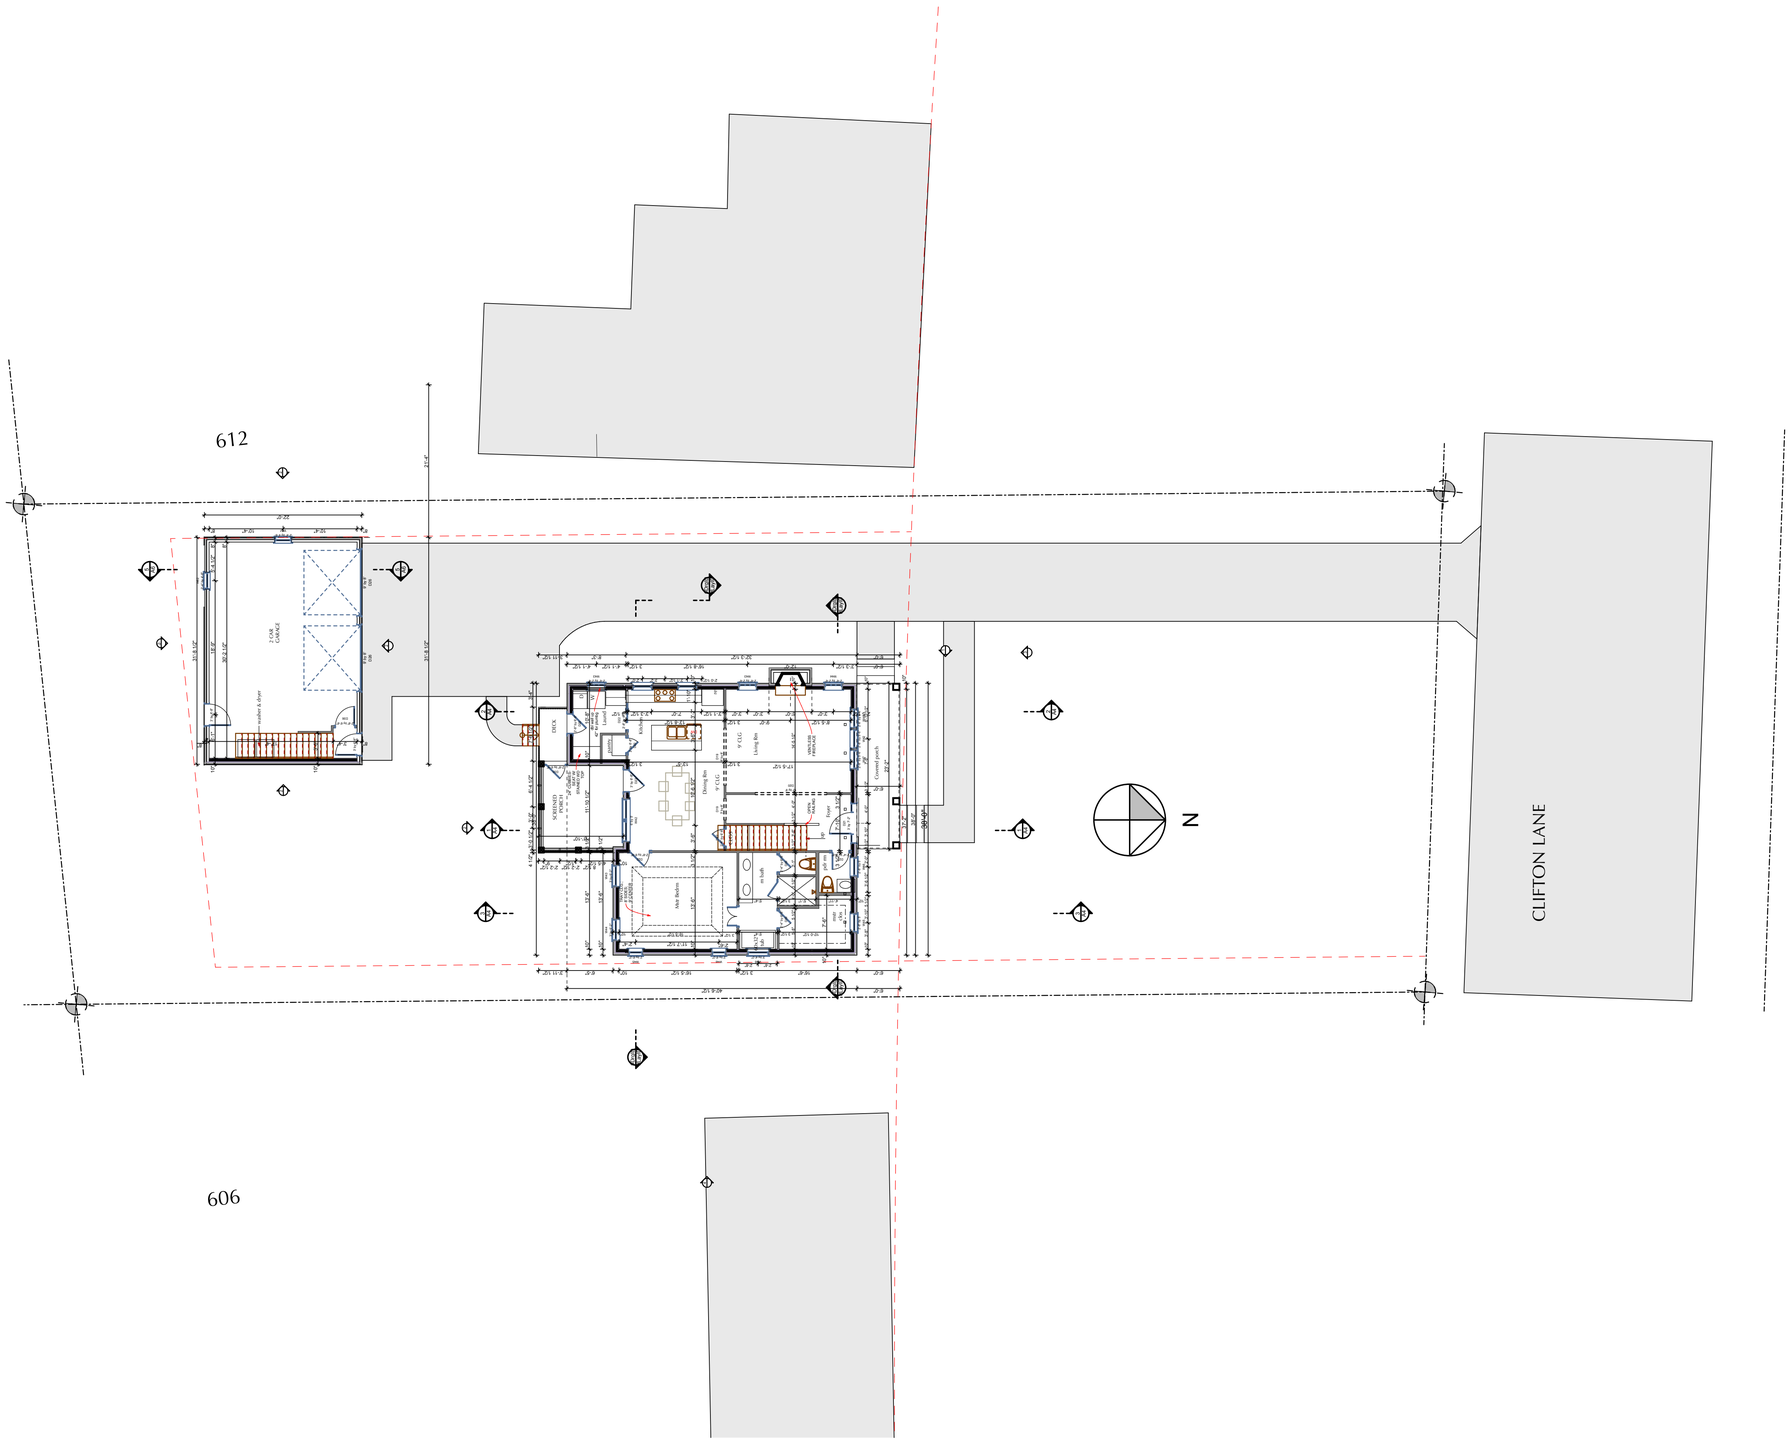

1 SITE PLAN
SCALE: 1" = 10'

PRESTON H. QUIRK
REGISTERED ARCHITECT
ARCHITECTURE
NO. 19849
STATE OF TENNESSEE
6/6/23

QUIRK DESIGNS
2931 BERRY HILL DRIVE
SUITE 200
NASHVILLE, TN 37204
Phone: (615) 269-9248 Fax: (615) 627-1298
email: quirkdesigns@comcast.net

New Residence
C. HARWELL
1413 Clifton Lane
Nashville , TN 37215

DATE: 6/6/23
REVISION

PROJECT NO: 15-110

COPYRIGHT 6/6/23
QUIRK DESIGNS

SITE PLAN

C1
SHEET 2

C. HARWELL
1413 Clifton Lane
Nashville , TN 37215

FLOOR AREA	
Zone Name	Area
1st flr	1,360
2nd flr	930
	2,290 sq ft

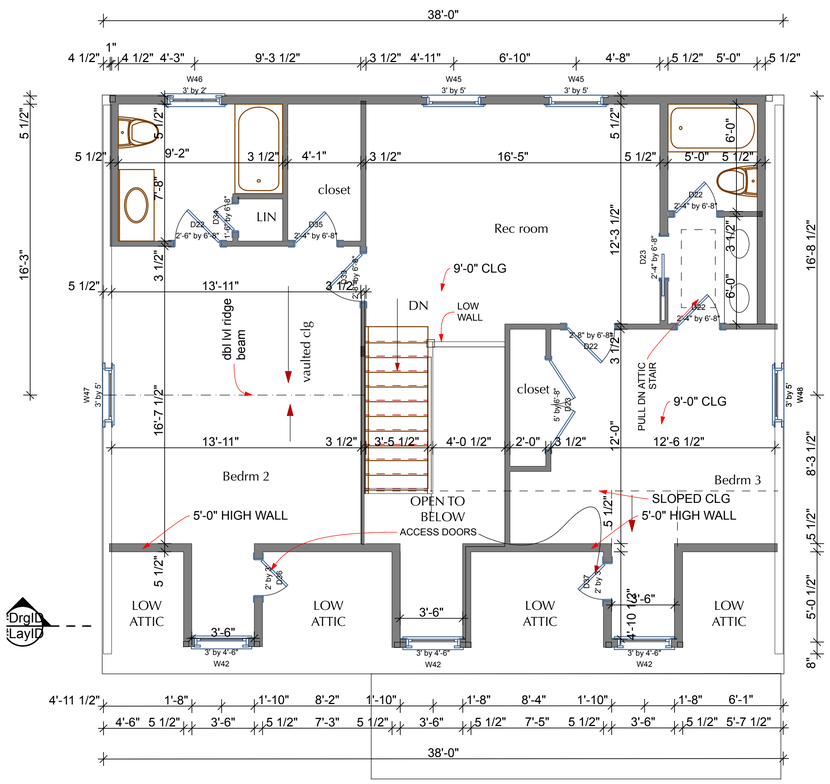

1 2ND FLR PLAN
SCALE: 1/4" = 1'-0"

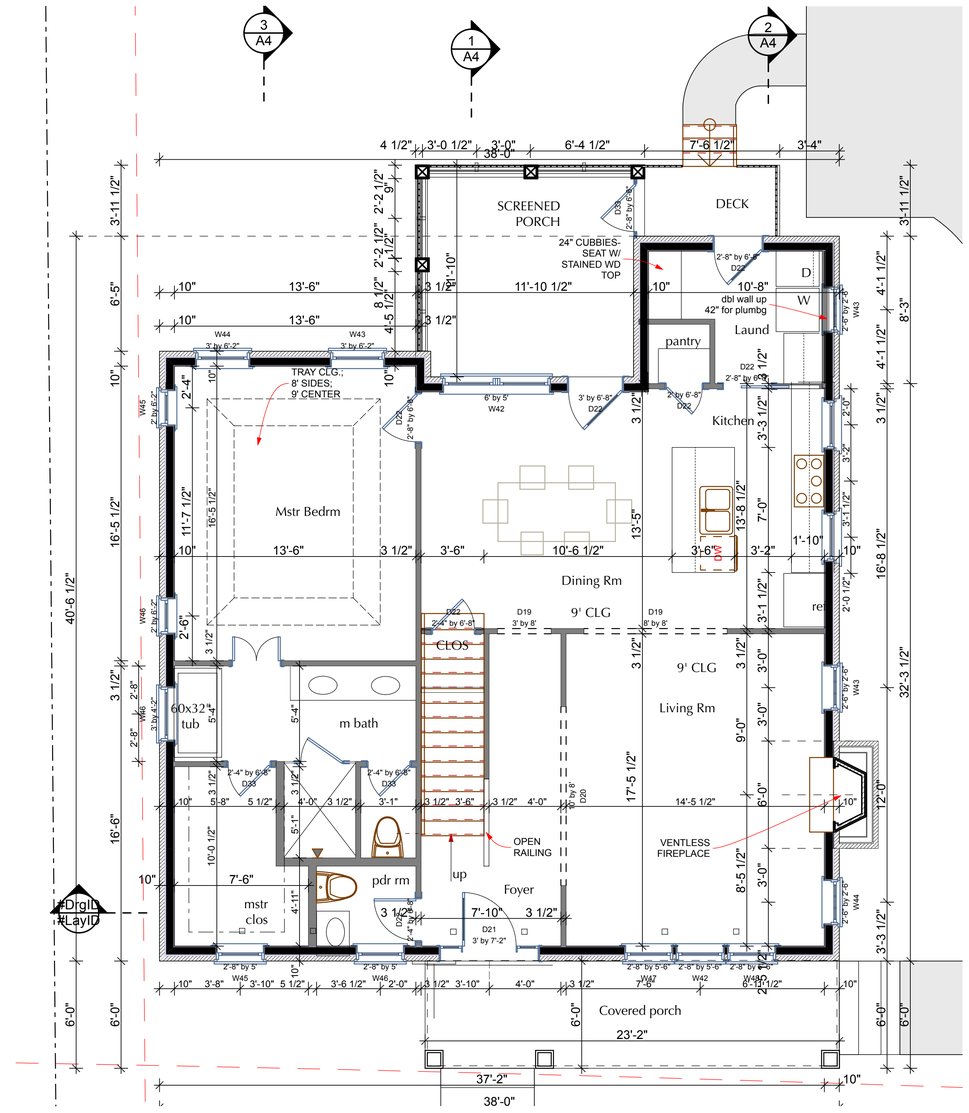

1 1ST FLOOR PLAN
SCALE: 1/4" = 1'-0"

QUIRK DESIGNS
2931 BERRY HILL DRIVE
SUITE 200
NASHVILLE, TN 37204
Phone: (615) 269-9246 Fax: (615) 627-1298
email: quirkdesigns@comcast.net

New Residence
C. HARWELL
1413 Clifton Lane
Nashville , TN 37215

DATE: 6/6/23
REVISION

PROJECT NO: 15-110

COPYRIGHT 6/6/23
QUIRK DESIGNS

FLOOR PLANS

A1
SHEET 3

C. HARWELL
1413 Clifton Lane
Nashville , TN 37215

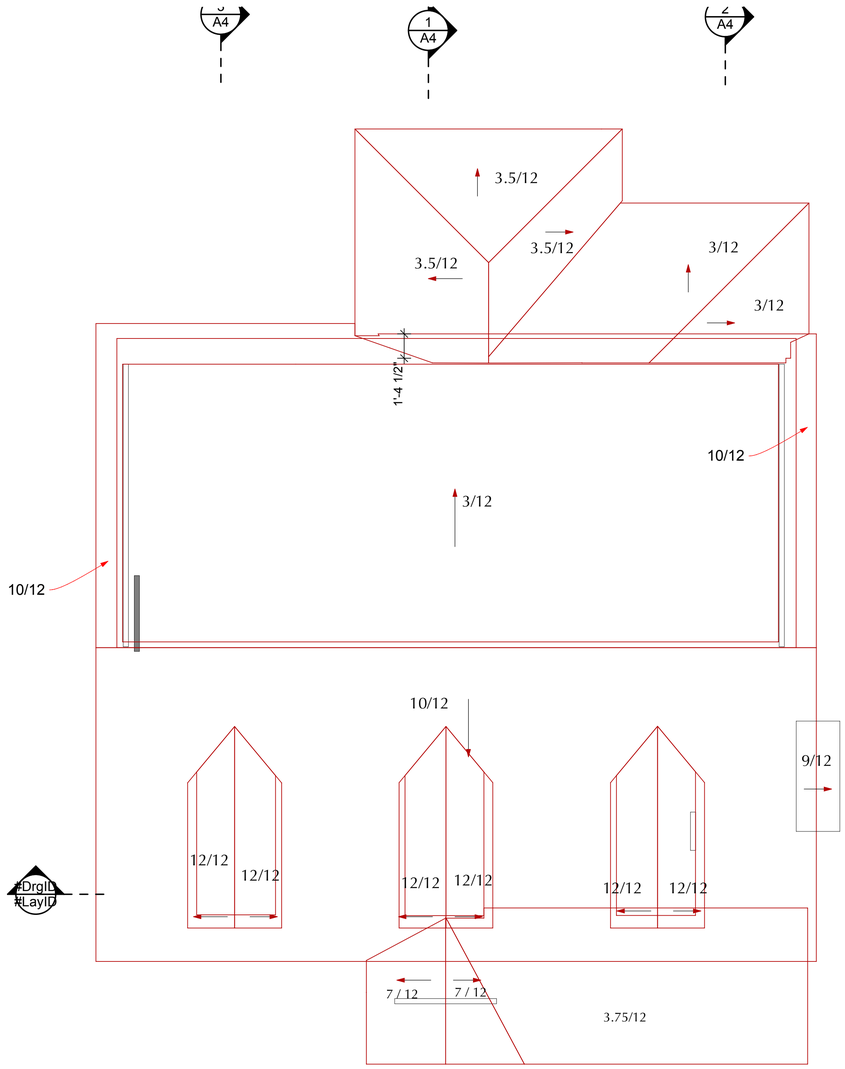

2 ROOF PLAN
SCALE: 1/4" = 1'-0"

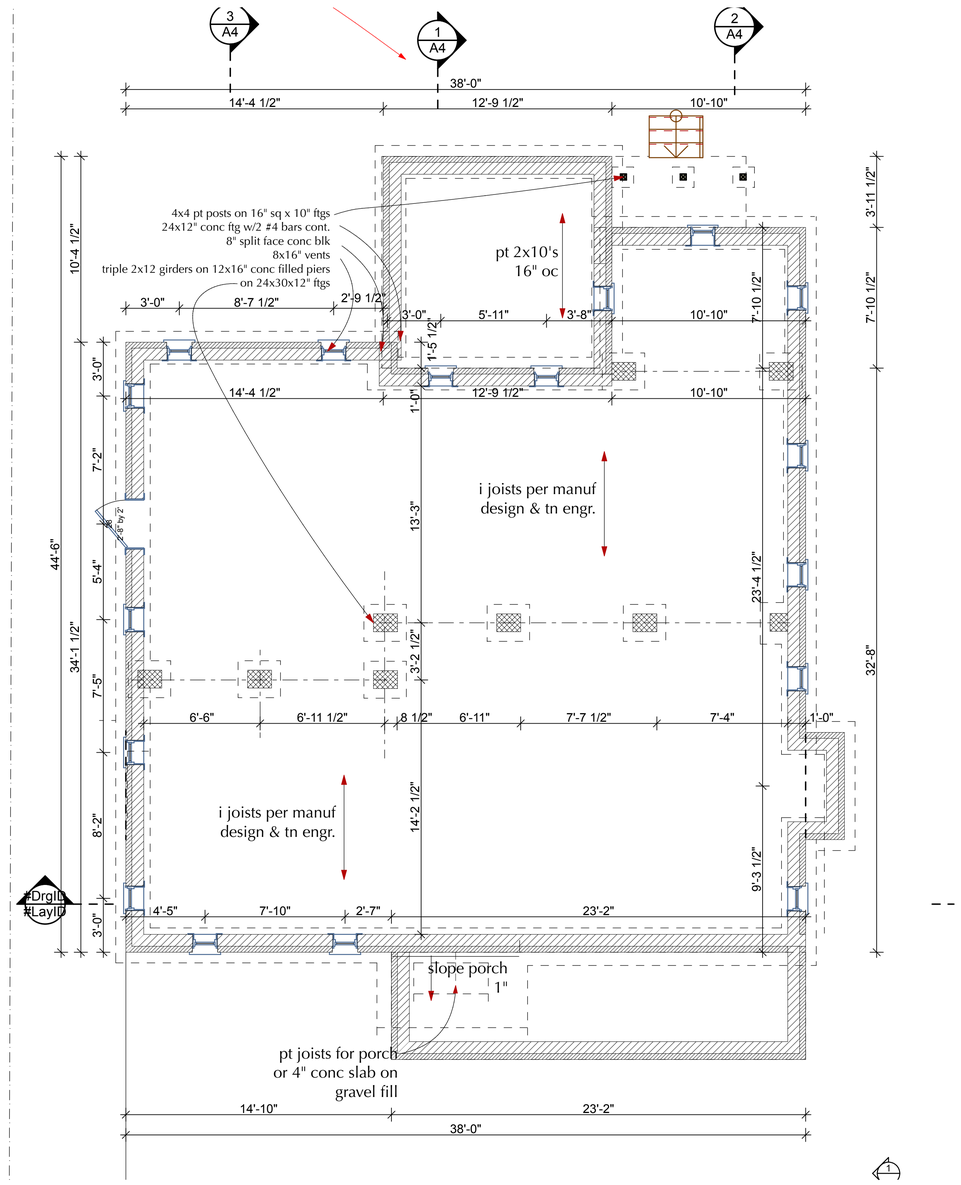

1 FOUNDATION PLAN
SCALE: 1/4" = 1'-0"

PRESTON H. QUIRK
REGISTERED ARCHITECT
AGRICULTURE
COMMERCE
NO. 19849
STATE OF TENNESSEE
6/6/23

QUIRK DESIGNS
2331 BERRY HILL DRIVE
SUITE 200
NASHVILLE, TN 37204
Phone: (615) 269-9246 Fax: (615) 627-1298
email: quirkdesigns@comcast.net

New Residence
C. HARWELL
1413 Clifton Lane
Nashville , TN 37215

DATE: 6/6/23
REVISION

PROJECT NO: 15-110

COPYRIGHT 6/6/23
QUIRK DESIGNS

FND & ROOF PLNS

A2
SHEET 4

C. HARWELL
1413 Clifton Lane
Nashville , TN 37215

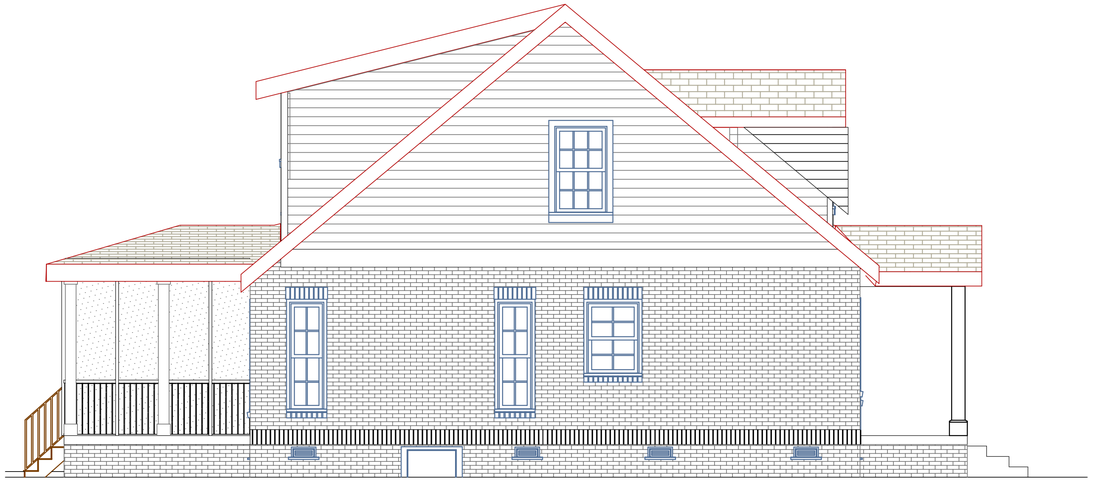

4 LEFT ELEVATION
SCALE: 1/4" = 1'-0"

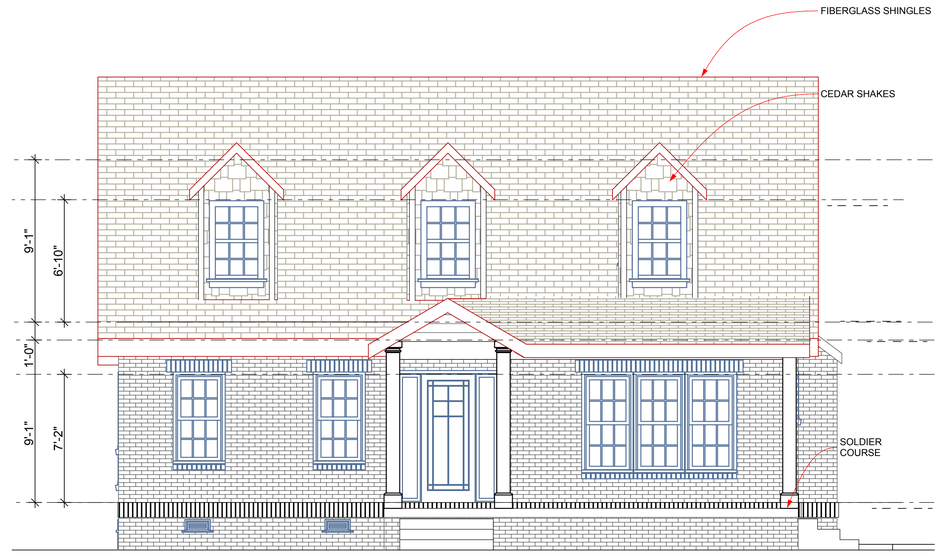

1 FRONT ELEVATION
SCALE: 1/4" = 1'-0"

2 REAR ELEVATION
SCALE: 1/4" = 1'-0"

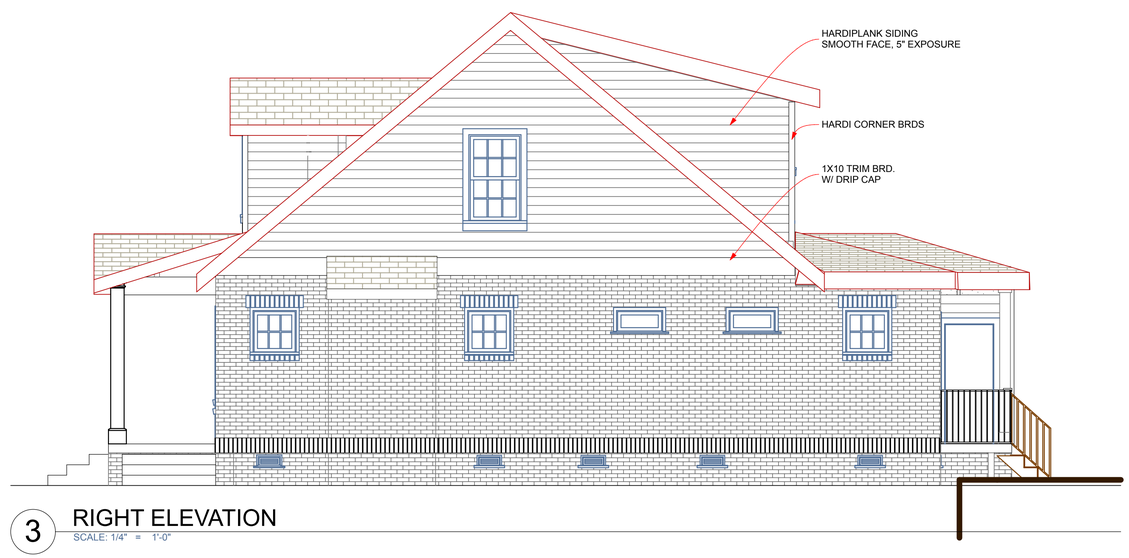

3 RIGHT ELEVATION
SCALE: 1/4" = 1'-0"

PRESTON H. QUIRK
REGISTERED ARCHITECT
TENNESSEE
NO. 19849
STATE OF TENNESSEE
6/6/23

QUIRK DESIGNS
2931 BERRY HILL DRIVE
SUITE 200
NASHVILLE, TN 37204
Phone: (615) 269-9246 Fax: (615) 627-1298
email: quirkdesigns@comcast.net

New Residence
C. HARWELL
1413 Clifton Lane
Nashville , TN 37215

DATE: 6/6/23
REVISION

PROJECT NO: 15-110

COPYRIGHT 6/6/23
QUIRK DESIGNS

ELEVATIONS

A3
SHEET 5

C. HARWELL
1413 Clifton Lane
Nashville , TN 37215

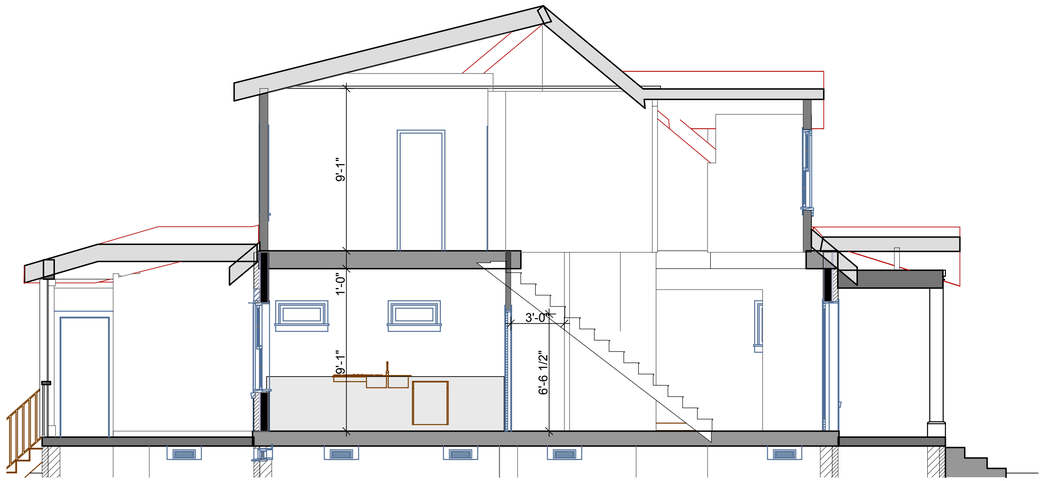

1 SECTION - STAIR
SCALE: 1/4" = 1'-0"

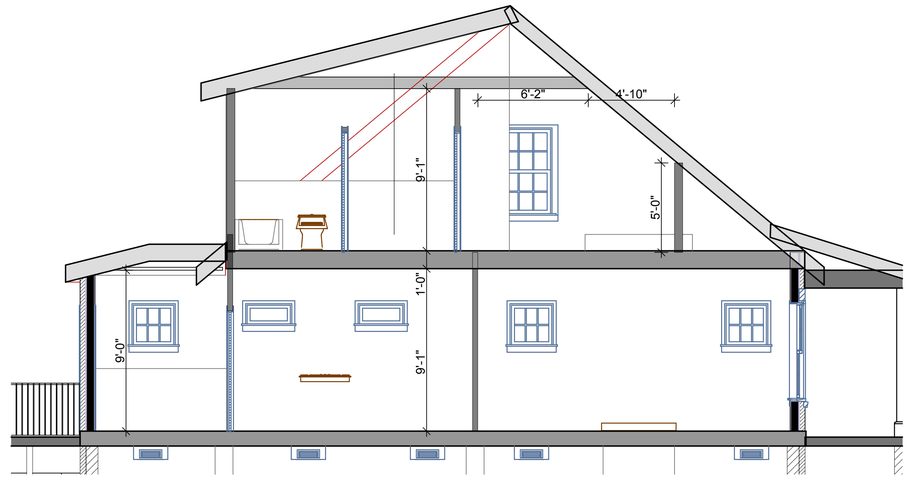

2 SECTION - RIGHT SIDE
SCALE: 1/4" = 1'-0"

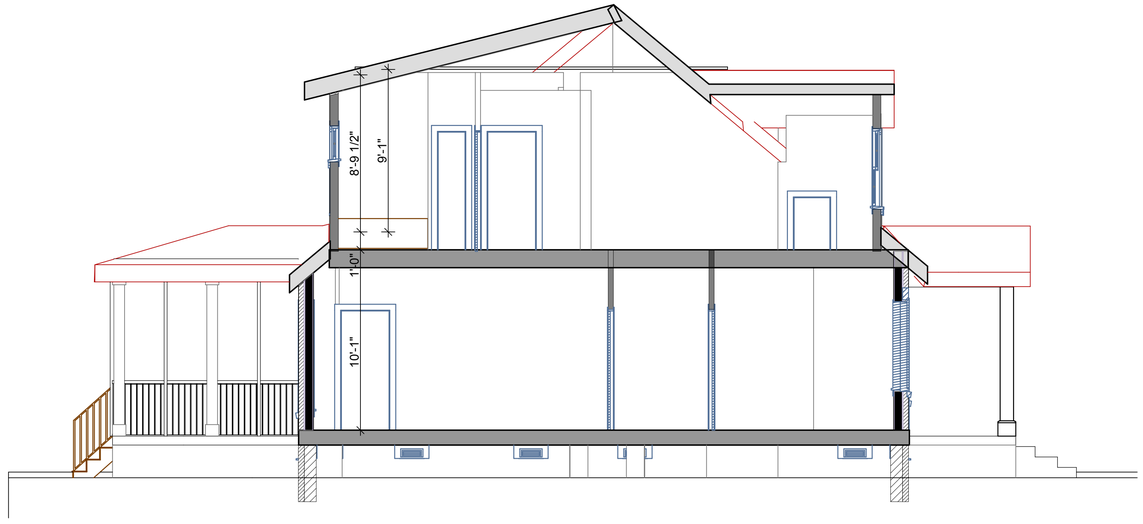

3 SECTION - MASTER BEDROOM
SCALE: 1/4" = 1'-0"

PRESTON H. QUIRK
REGISTERED ARCHITECT
ARCHITECTURE
COMMERCE
NO. 19849
STATE OF TENNESSEE
6/6/23

2331 BERRY HILL DRIVE
SUITE 200
NASHVILLE, TN 37204
Phone: (615) 269-9246 Fax: (615) 627-1298
email: quirkdesigns@comcast.net

QUIRK DESIGNS

New Residence
C. HARWELL
1413 Clifton Lane
Nashville , TN 37215

DATE: 6/6/23
REVISION

PROJECT NO: 15-110

COPYRIGHT 6/6/23
QUIRK DESIGNS

SECTIONS

A4
SHEET 6

C. HARWELL
1413 Clifton Lane
Nashville , TN 37215

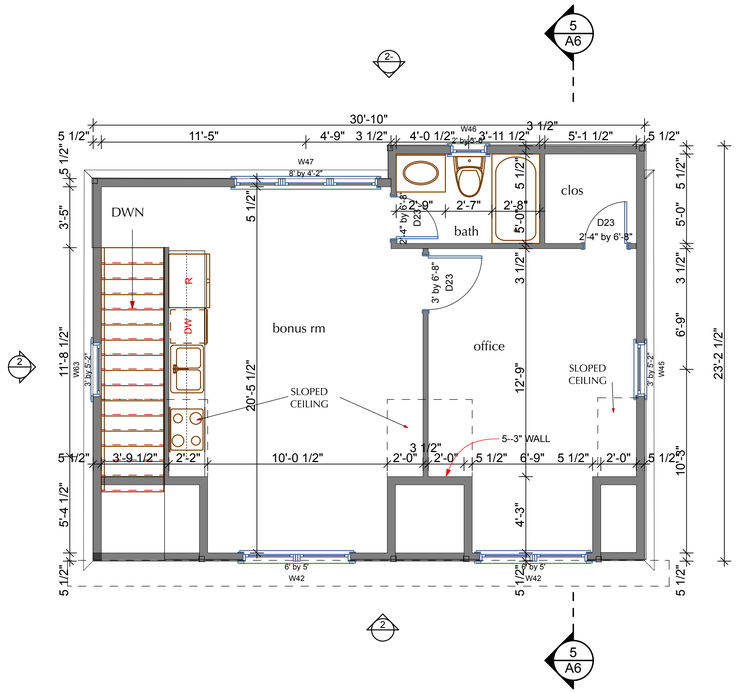

4 2ND FLR PLAN (1)
SCALE: 1/4" = 1'-0"

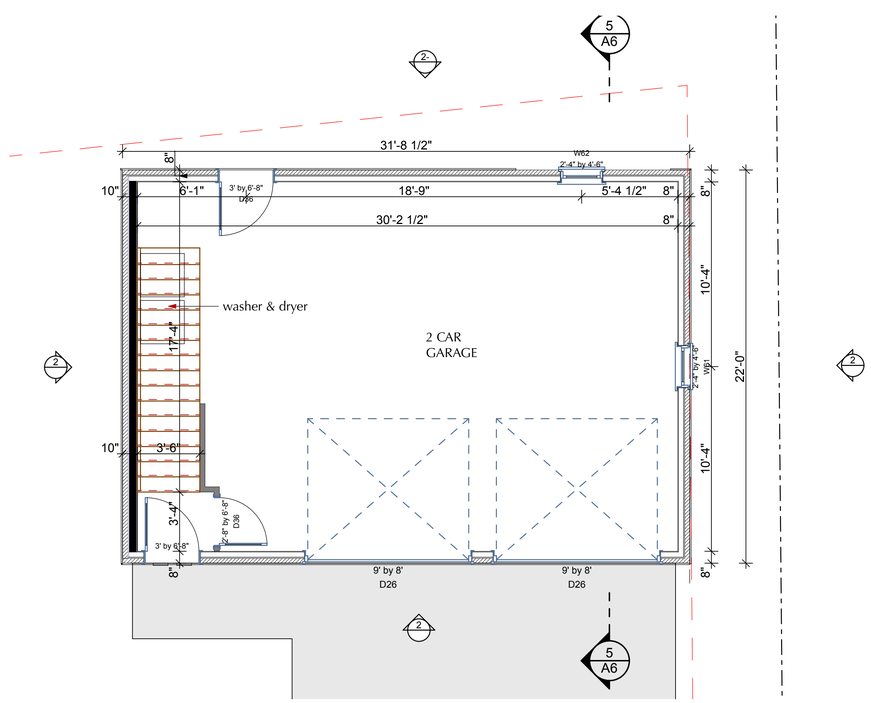

1 1ST FLOOR PLAN
SCALE: 1/4" = 1'-0"

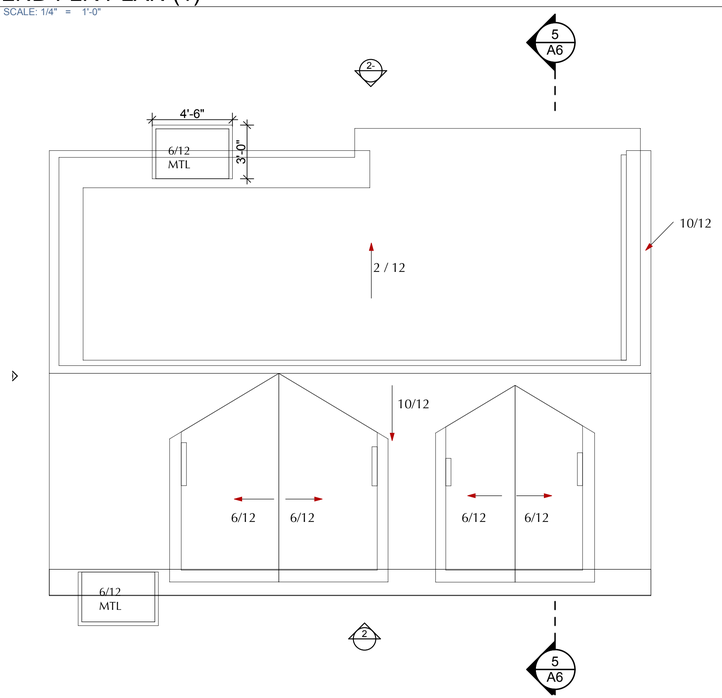

3 ROOF PLAN
SCALE: 1/4" = 1'-0"

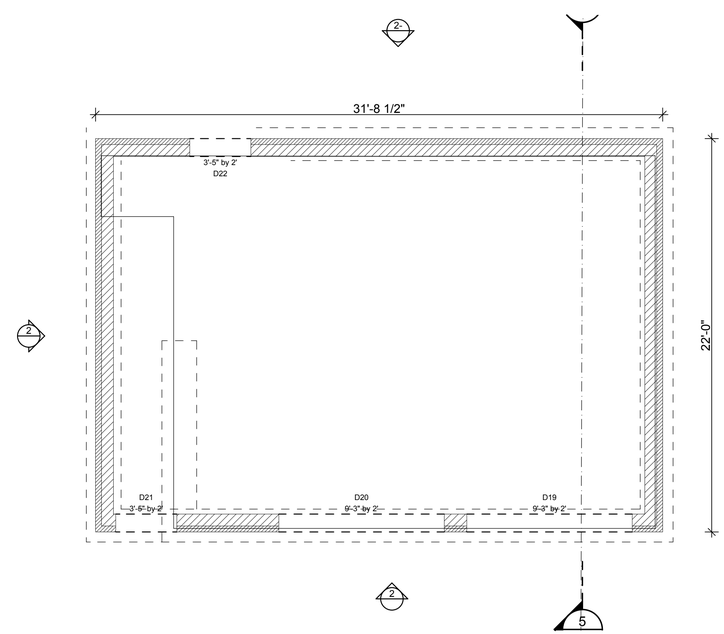

2 FOUNDATION PLAN
SCALE: 1/4" = 1'-0"

PRESTON H. QUIRK
REGISTERED ARCHITECT
AGRICULTURE
COMMERCE
NO. 19849
STATE OF TENNESSEE
6/6/23

QUIRK DESIGNS
2931 BERRY HILL DRIVE
SUITE 200
NASHVILLE, TN 37204
Phone: (615) 269-9246 Fax: (615) 627-1298
email: quirkdesigns@comcast.net

New Residence
C. HARWELL
1413 Clifton Lane
Nashville , TN 37215

DATE: 6/6/23
REVISION

PROJECT NO: 15-110

COPYRIGHT 6/6/23
QUIRK DESIGNS

GARAGE PLANS

A5
SHEET 7

C. HARWELL
1413 Clifton Lane
Nashville , TN 37215

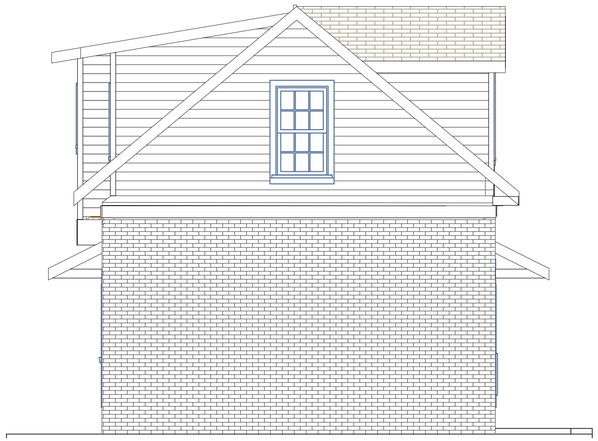

3 GARAGE LEFT
SCALE: 1/4" = 1'-0"

1 GARAGE FRONT
SCALE: 1/4" = 1'-0"

4 GARAGE RIGHT
SCALE: 1/4" = 1'-0"

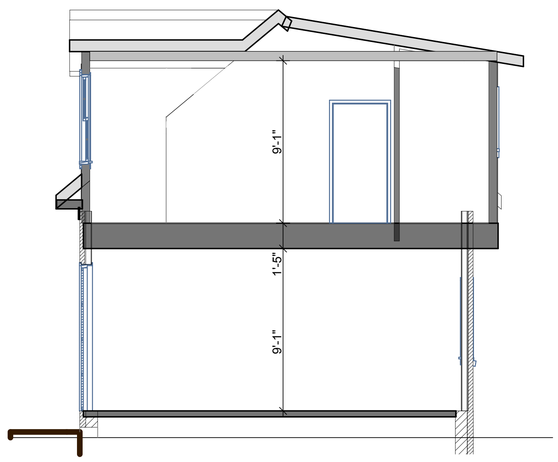

5 GARAGE SECTION
SCALE: 1/4" = 1'-0"

2 GARAGE REAR
SCALE: 1/4" = 1'-0"

PRESTON H. QUIRK
REGISTERED ARCHITECT
TENNESSEE
NO. 19849
STATE OF TENNESSEE
6/6/23

2931 BERRY HILL DRIVE
SUITE 200
NASHVILLE, TN 37204
Phone: (615) 269-9246 Fax: (615) 627-1298
email: quirkdesigns@comcast.net
QUIRK DESIGNS

New Residence
C. HARWELL
1413 Clifton Lane
Nashville , TN 37215

DATE: 6/6/23
REVISION

PROJECT NO: 15-110

COPYRIGHT 6/6/23
QUIRK DESIGNS

GARAGE ELEVATIONs
SECTION

A6
SHEET 8