111 PAGE ROAD

NASHVILLE, TN

BINKLEY DESIGNED
4630 COLUMBIA PIKE
THOMPSONS STATION, TN
37179

PHONE: 407.451.1344
TURNER@BINKLEYDESIGNED.COM

111 PAGE ROAD

NASHVILLE, TN

BINKLEY DESIGNED

REV.	DATE

DATE: 06/23/2025

PROJECT NUMBER:

DRAWN BY: KC

CHECKED BY: TB

SHEET TITLE: COVER

SHEET NUMBER: A0

CONSTRUCTION DOCUMENTS

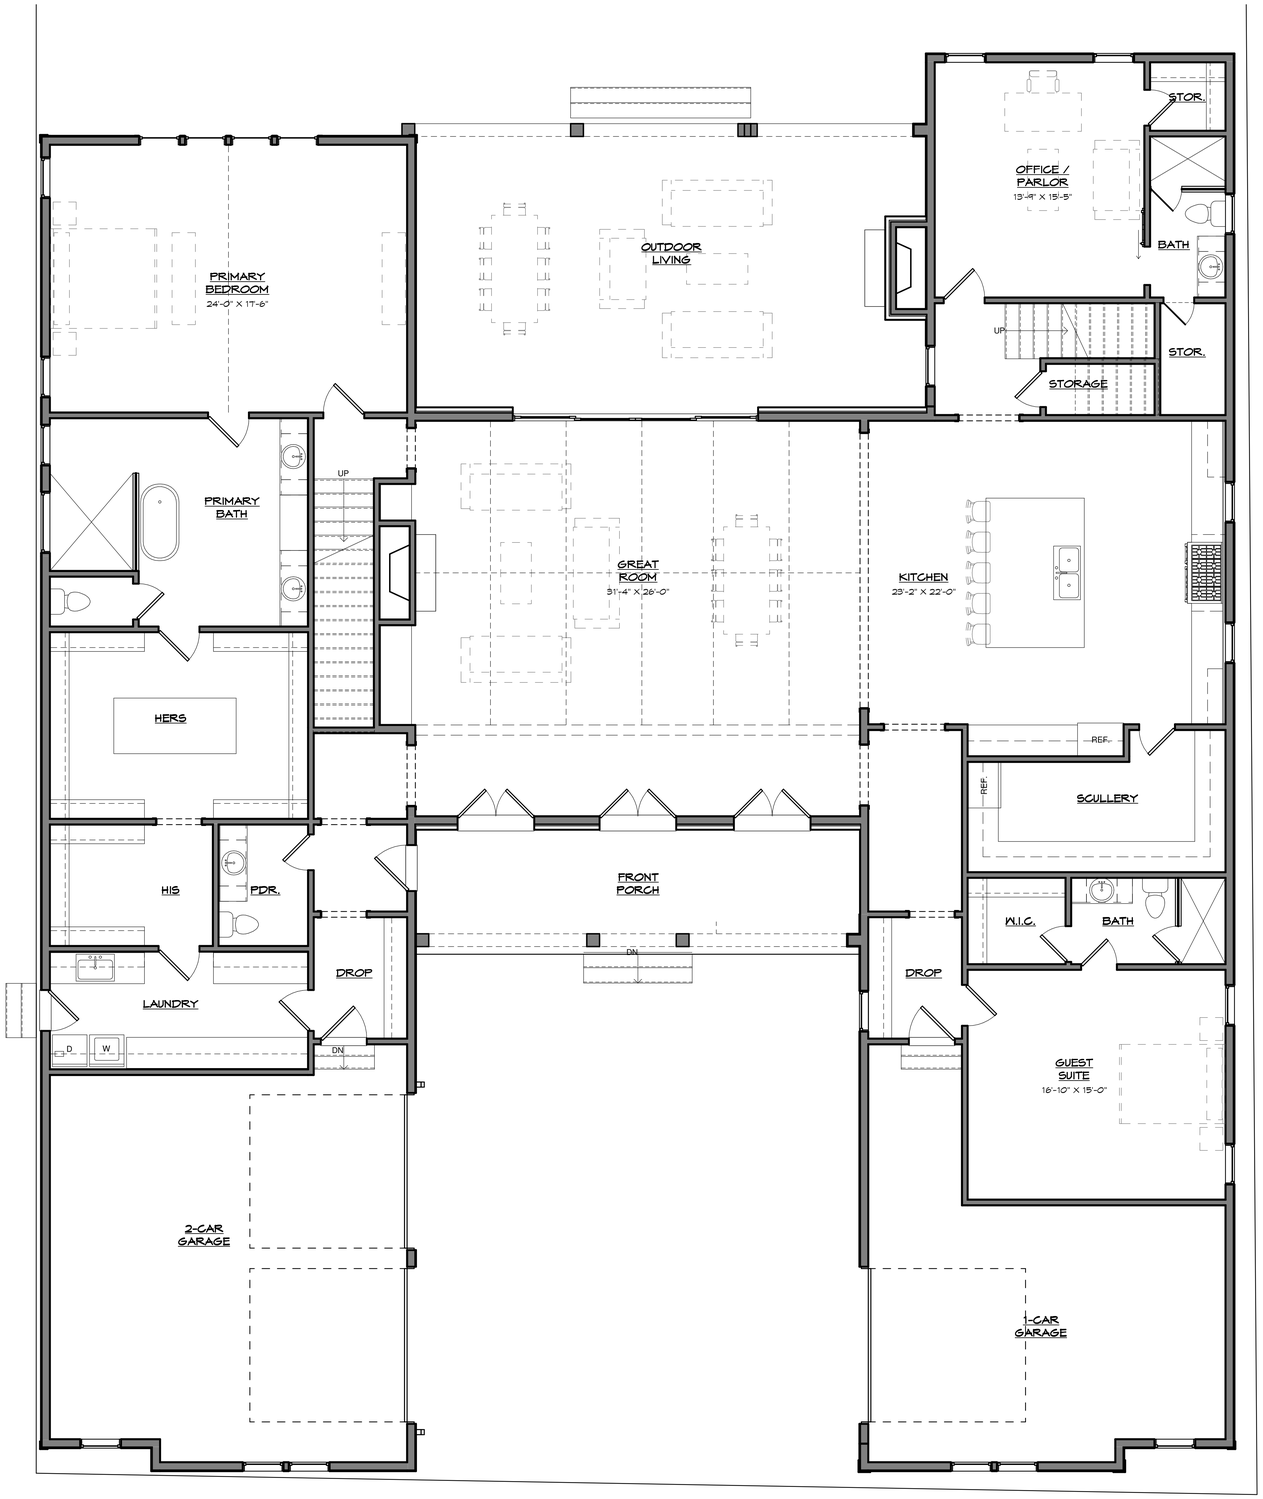

1 FIRST FLOOR PLAN
1/4" = 1'-0"

10'-0" CEILING HEIGHT UNLESS NOTED OTHERWISE 0' 2' 4' 8'

NOTE:
BUILDER TO COODINATE FINAL PORCH & STAIRS WITH GRADING PLAN AND LANDSCAPE ARCHITECTS DRAWINGS

NOTE:
REFER TO FRAMING PACKAGE FOR ALL JOIST ORIENTATION & SPACING, TYPICAL ALL LOCATIONS. SUPPLEMENT & SIZE BEAMS PER STRUCTURAL ENGINEER

AREA CALCULATIONS

BASED ON OUTSIDE FACE OF STUD OR BLOCK

HEATED	
FIRST FLOOR	3852 SF
SECOND FLOOR	3364 SF
HEATED	7215 SF
GRAND TOTAL	7215 SF

BINKLEY DESIGNED
4630 COLUMBIA PIKE
THOMPSONS STATION, TN
37179
PHONE: 407.451.1344
TURNER@BINKLEYDESIGNED.COM

111 PAGE ROAD
NASHVILLE, TN
BINKLEY DESIGNED

REV.	DATE

DATE: 06/23/2025
PROJECT NUMBER:
DRAWN BY: KC
CHECKED BY: TB

SHEET TITLE: FIRST FLOOR PLAN
SHEET NUMBER: A3

CONSTRUCTION DOCUMENTS

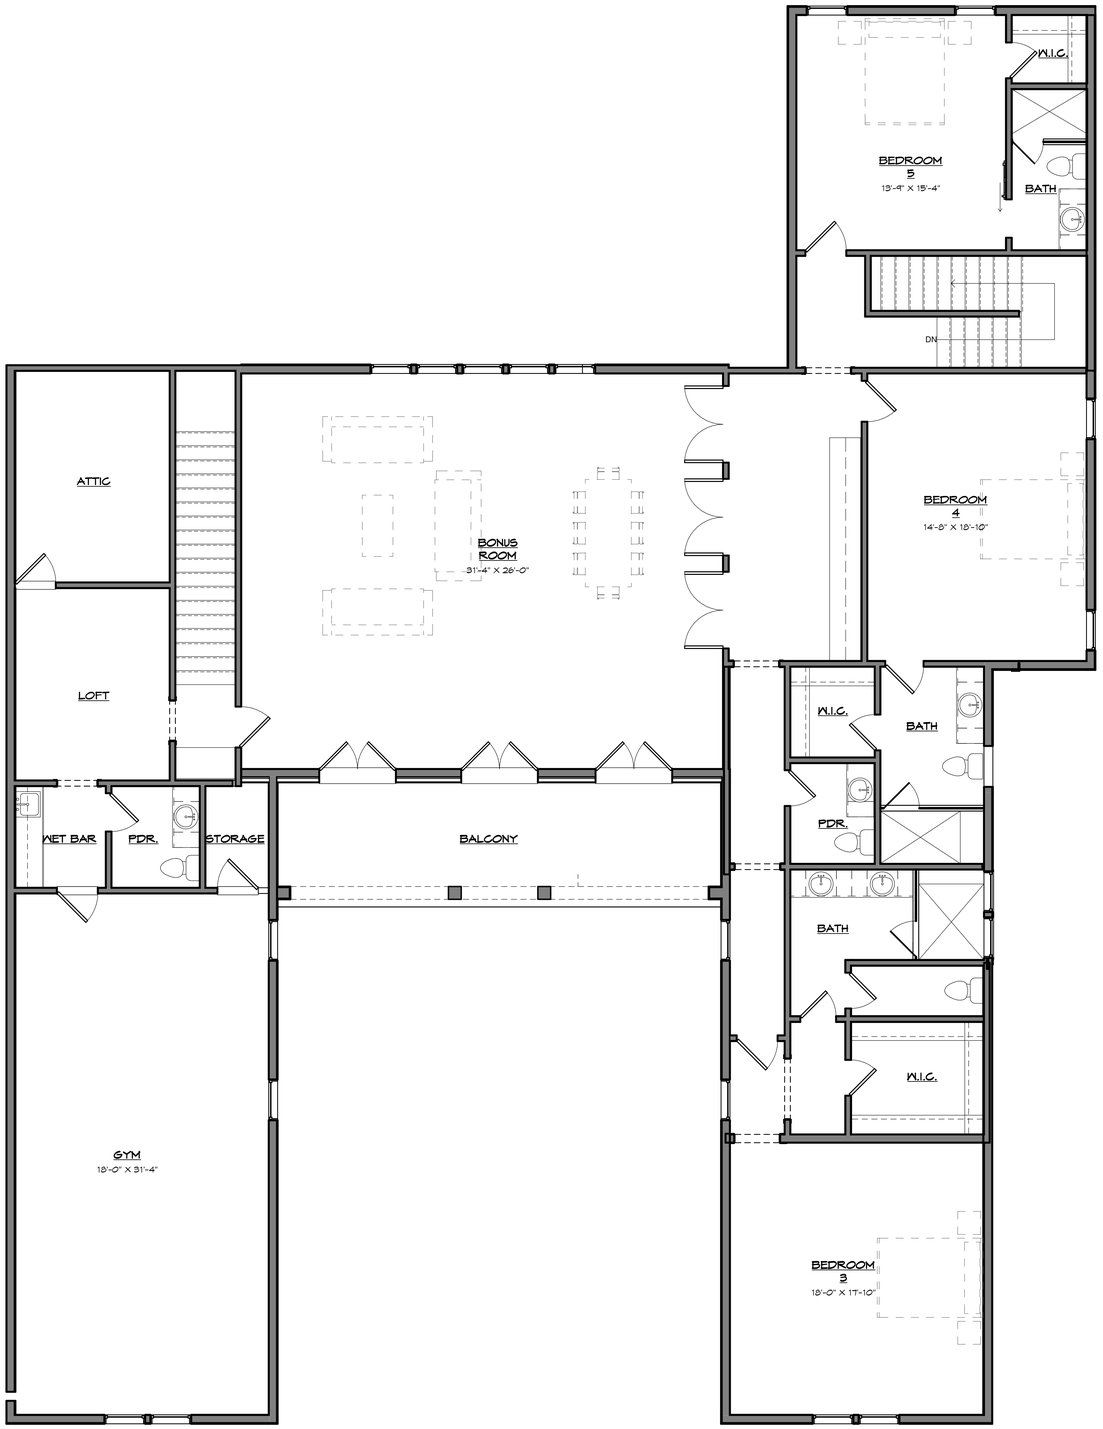

1 SECOND FLOOR PLAN
1/4" = 1'-0"

9'-0" CEILING HEIGHT UNLESS NOTED OTHERWISE

0' 2' 4' 8'

NOTE:
BUILDER TO COODINATE FINAL PORCH & STAIRS WITH GRADING PLAN AND LANDSCAPE ARCHITECTS DRAWINGS

NOTE:
REFER TO FRAMING PACKAGE FOR ALL JOIST ORIENTATION & SPACING, TYPICAL ALL LOCATIONS. SUPPLEMENT & SIZE BEAMS PER STRUCTURAL ENGINEER

AREA CALCULATIONS

BASED ON OUTSIDE FACE OF STUD OR BLOCK	
HEATED	
FIRST FLOOR	3852 SF
SECOND FLOOR	3364 SF
HEATED	7215 SF
GRAND TOTAL	7215 SF

BINKLEY DESIGNED
4630 COLUMBIA PIKE
THOMPSONS STATION, TN
37179
PHONE: 407.451.1344
TURNER@BINKLEYDESIGNED.COM

111 PAGE ROAD
NASHVILLE, TN
BINKLEY DESIGNED

REV.	DATE

DATE: 06/23/2025
PROJECT NUMBER:
DRAWN BY: KC
CHECKED BY: TB

SHEET TITLE: SECOND FLOOR PLAN
SHEET NUMBER: A4

CONSTRUCTION DOCUMENTS