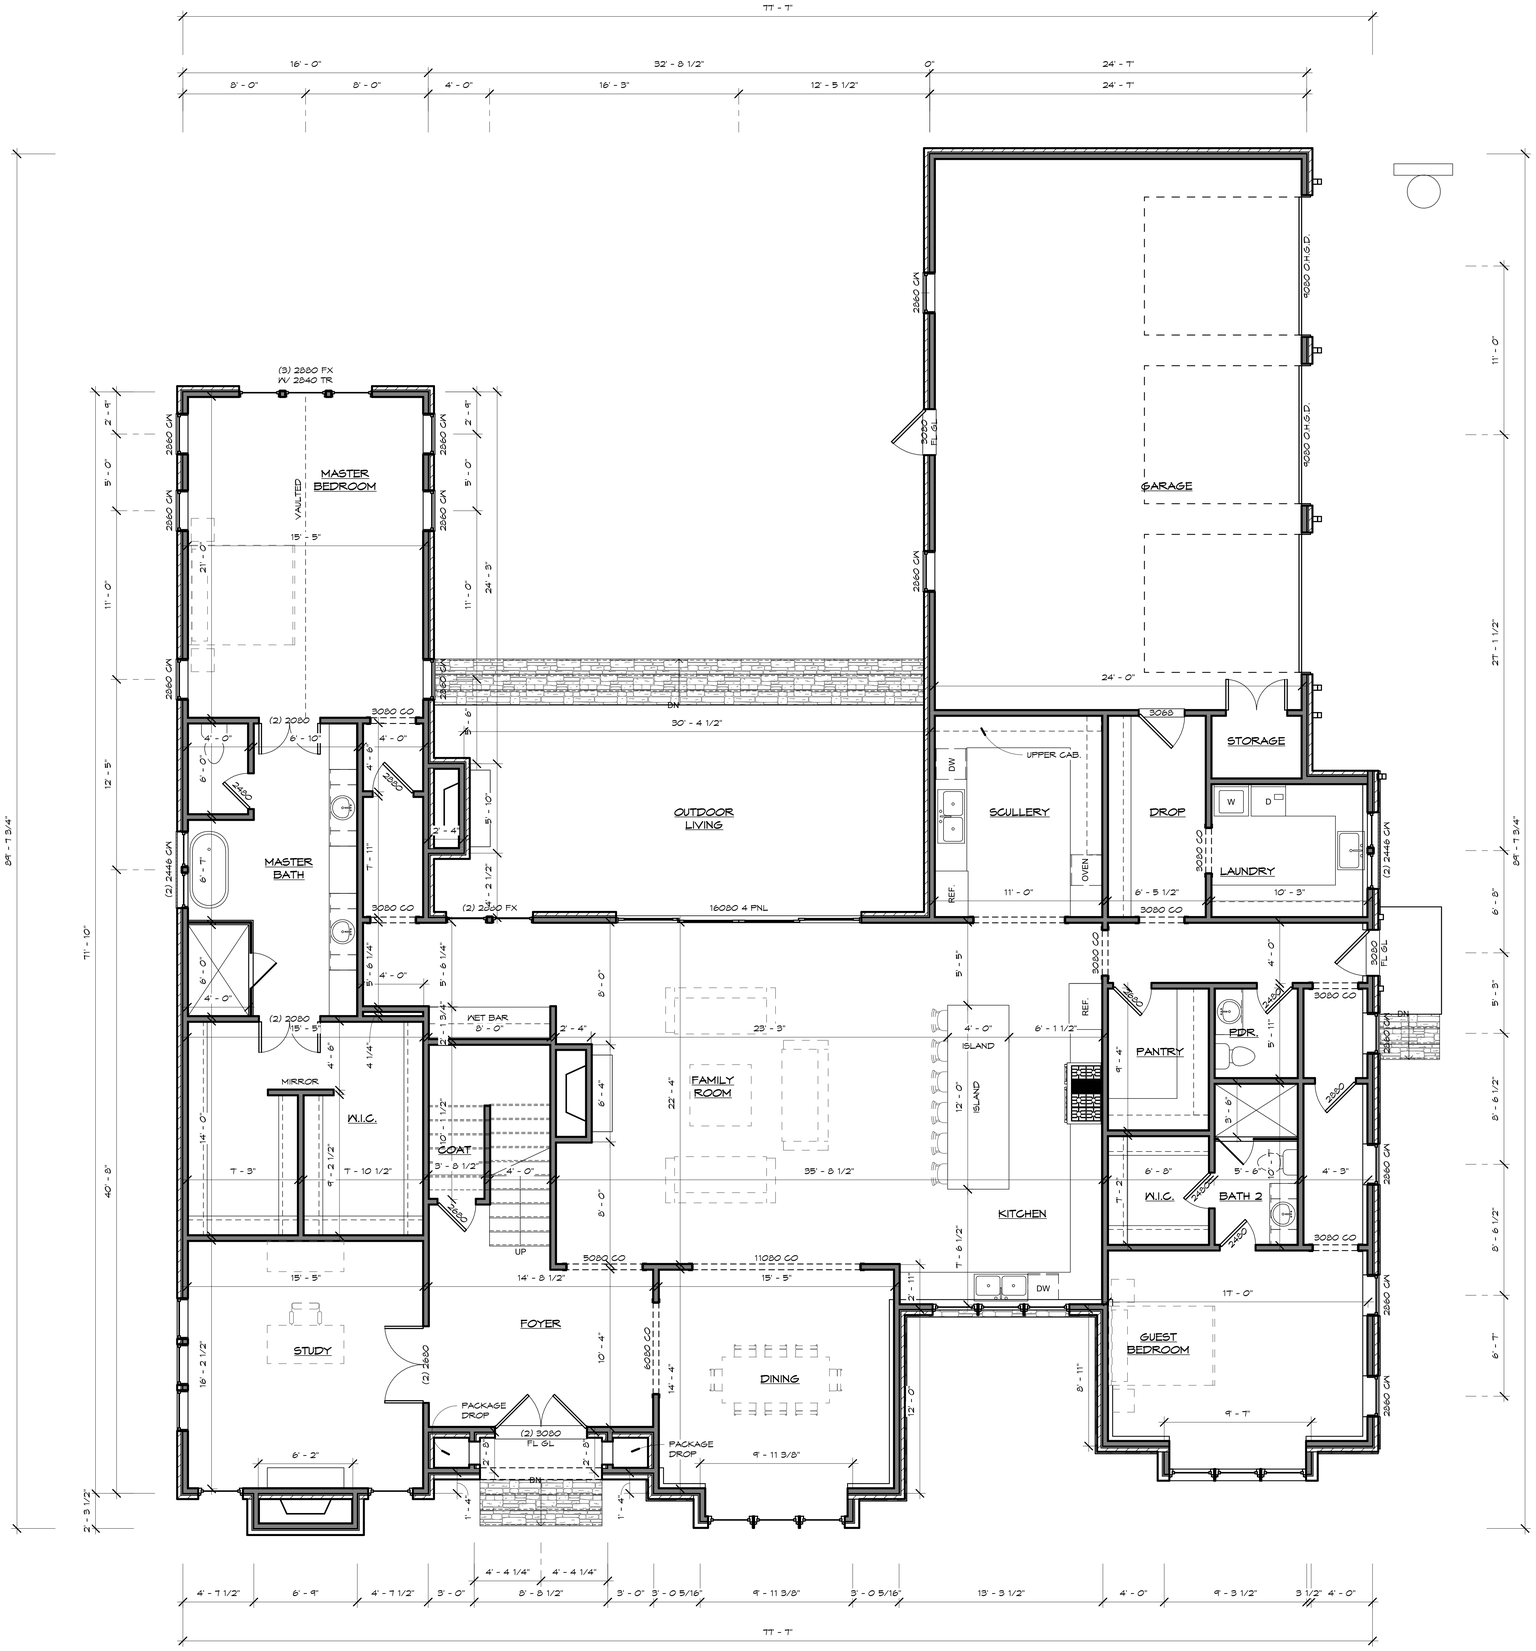

1 FIRST FLOOR PLAN
1/4" = 1'-0"

0' 2' 4' 8'

AREA CALCULATIONS

HEATED	
FIRST FLOOR	3609 SF
SECOND FLOOR	2050 SF
TOTAL HEATED	
BASED ON OUTSIDE FACE OF STUD OR BLOCK	
OPTIONAL	
ATTIC/OPTIONAL BUILD-OUT	456 SF
OPTIONAL	456 SF
UNHEATED	
OUTDOOR LIVING	454 SF
GARAGE	880 SF
ENTRY	38 SF
UNHEATED	1372 SF
GRAND TOTAL	7487 SF

NOTE:
BUILDER TO COODINATE FINAL PORCH & STAIRS WITH GRADING PLAN AND LANDSCAPE ARCHITECTS DRAWINGS

NOTE:
REFER TO FRAMING PACKAGE FOR ALL JOIST ORIENTATION & SPACING, TYPICAL ALL LOCATIONS. SUPPLEMENT & SIZE BEAMS PER STRUCTURAL ENGINEER

BINKLEY DESIGNED
5017 ALPACA DRIVE
SPRING HILL, TN 37174
PHONE: 618.626.4230
TURNER@BINKLEYDESIGNED.COM

CATALYST HOMES

126 TAGGART AVENUE
NASHVILLE, TN

REV.	DATE

DATE: 12/29/2025

PROJECT NUMBER:

DRAWN BY: HML

CHECKED BY:

SHEET TITLE: FIRST FLOOR PLAN

SHEET NUMBER: A2

PRICING SET

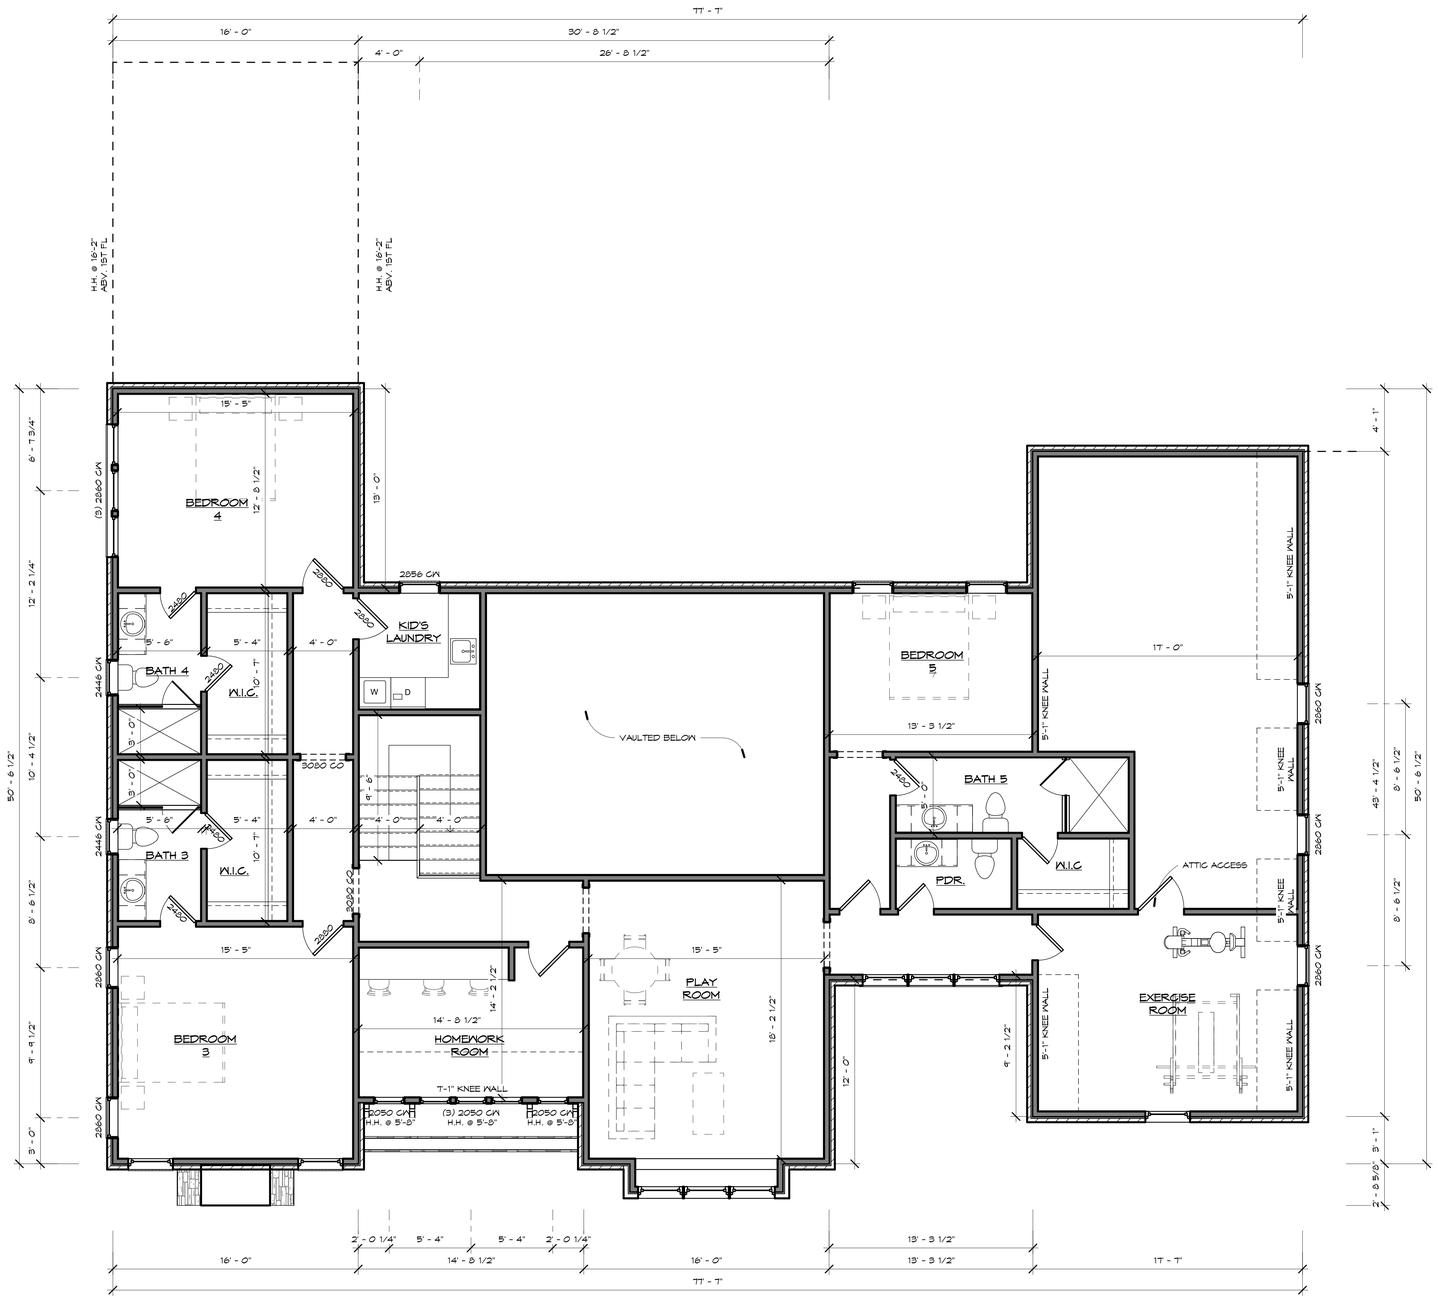

1 SECOND FLOOR PLAN
1/4" = 1'-0"

0' 2' 4' 8'

AREA CALCULATIONS

BASED ON OUTSIDE FACE OF STUD OR BLOCK

HEATED	
FIRST FLOOR	3609 SF
SECOND FLOOR	2050 SF
HEATED	5659 SF
OPTIONAL	
ATTIC/OPTIONAL BUILD-OUT	456 SF
OPTIONAL	456 SF
UNHEATED	
OUTDOOR LIVING	454 SF
GARAGE	880 SF
ENTRY	38 SF
UNHEATED	1372 SF
GRAND TOTAL	7487 SF

NOTE:
BUILDER TO COODINATE FINAL PORCH & STAIRS WITH GRADING PLAN AND LANDSCAPE ARCHITECTS DRAWINGS

NOTE:
REFER TO FRAMING PACKAGE FOR ALL JOIST ORIENTATION & SPACING, TYPICAL ALL LOCATIONS. SUPPLEMENT & SIZE BEAMS PER STRUCTURAL ENGINEER

BINKLEY DESIGNED
1017 ALPACA DRIVE
SPRING HILL, TN 37174
PHONE: 615.626.1230
TURNER@BINKLEYDESIGNED.COM

CATALYST HOMES
126 TAGART AVENUE
NASHVILLE, TN

REV.	DATE

DATE: 12/29/2025
PROJECT NUMBER:
DRAWN BY: HML
CHECKED BY:
SHEET TITLE: SECOND FLOOR PLAN
SHEET NUMBER: A3

PRICING SET

DOWNSPOUT NOTE:

DOWNSPOUTS NOT SHOWN FOR CLARITY. BUILDER TO PROVIDE DOWNSPOUTS IN COMPLIANCE W/ IRC REQUIREMENTS.

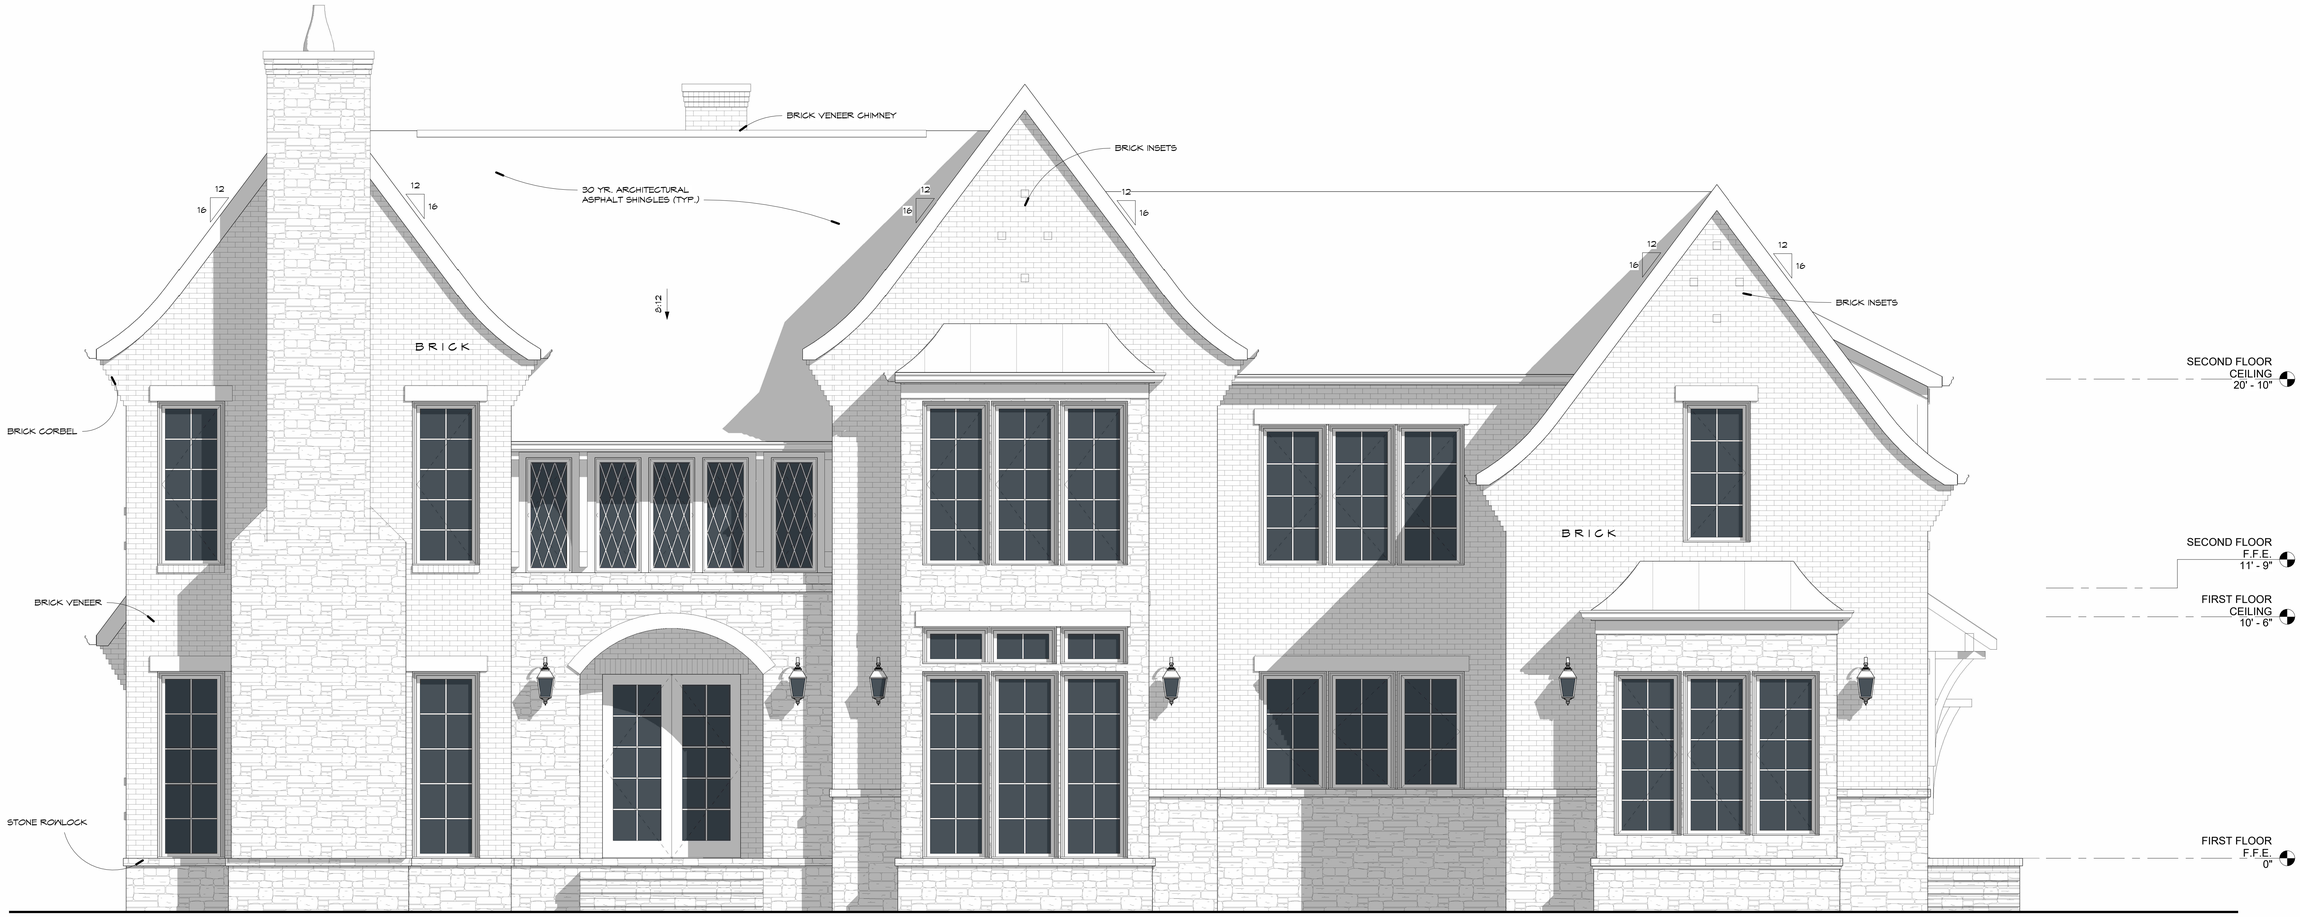

1 FRONT ELEVATION
3/8" = 1'-0"

BINKLEY DESIGNED
5017 ALPACA DRIVE
SPRING HILL, TN 37174
PHONE: 615.626.1230
TURNER@BINKLEYDESIGNED.COM

CATALYST HOMES
126 TAGGART AVENUE
NASHVILLE, TN

REV.	DATE

DATE: 12/29/2025
PROJECT NUMBER:
DRAWN BY: HML
CHECKED BY:
SHEET TITLE: ELEVATIONS
SHEET NUMBER: A5

PRICING SET