New Custom HPR Home

located at

1421B Rosebank Avenue
Nashville, Tennessee 37216

architect • jim myatt

MYATT ARCHITECTURE

SHEET INDEX

	COVER SHEET
A1.1	FOUNDATION PLAN
A2.1	1ST FLOOR PLAN
A2.2	2ND FLOOR PLAN & ROOF PLAN
A3.1	FRONT & RIGHT SIDE EXTERIOR ELEVATIONS
A3.2	REAR & LEFT SIDE EXTERIOR ELEVATIONS

REVISED ISSUE SET

FEBRUARY 09, 2026

NOTE:
CONTRACTOR SHALL VERIFY ALL CONDITIONS AND DIMENSIONS AT SITE BEFORE BEGINNING CONSTRUCTION, ANY DESCREPANCIES SHALL BE REPORTED TO JIM MYATT ARCHITECTURE FOR JUSTIFICATION AND/OR CORRECTION BEFORE PROCEEDING WITH WORK. CONTRACTOR SHALL ASSUME RESPONSIBILITY FOR ERRORS THAT ARE NOT REPORTED.

ALL FOOTINGS TO BE BELOW FROST LINE AND MUST REST ON UNDISTURBED SOIL CAPABLE OF HANDLING THE BUILDING.

MINIMUM FOUNDATION WALL – SEE DETAIL

HEAT/AIR DUCT AND OUTLET PLACEMENT PER OWNER, CONTRACTOR AND/OR SUPPLIER.

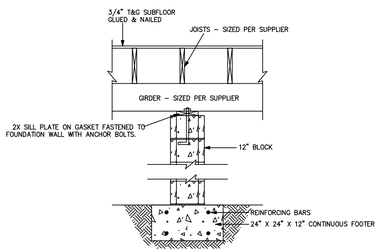

TYPICAL GIRDER SUPPORT

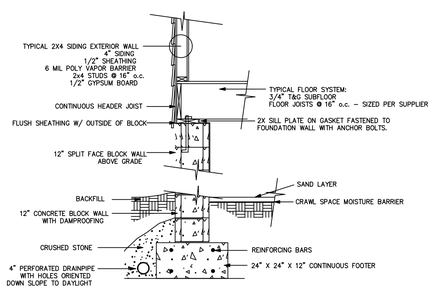

TYPICAL GIRDER SUPPORT

NOTE:
5% GRADE SLOPE AWAY FROM HOUSE IN ALL DIRECTIONS

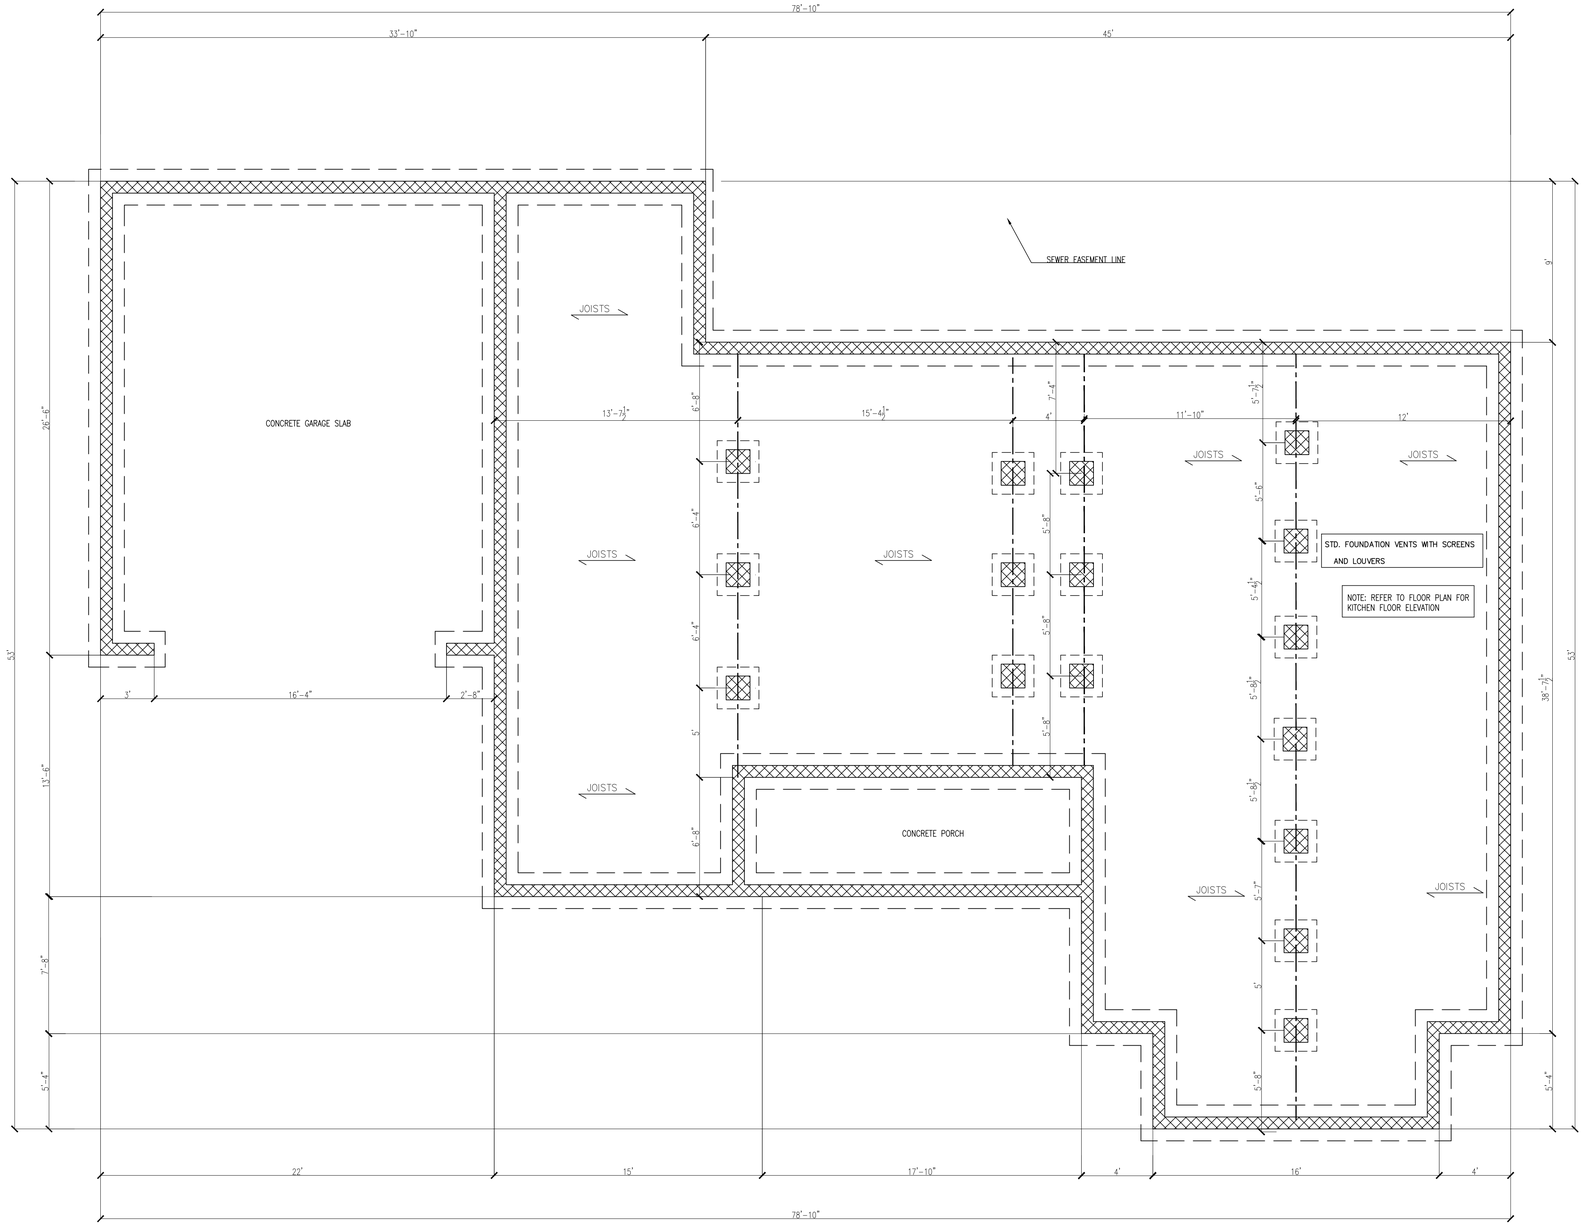

FOUNDATION PLAN $\frac{1}{4}$" = 1'-0"

MYATT ARCHITECTURE

REVISED ISSUE

NEW HOUSE PLANS:
1421B ROSEBANK AVENUE
NASHVILLE TN, 37216

REVISIONS	
DATE	DESCRIPTION

PROJECT NO.	
DATE	02/09/2026
DRAWN BY	J. MYATT RA
CHECKED BY	

A1.1

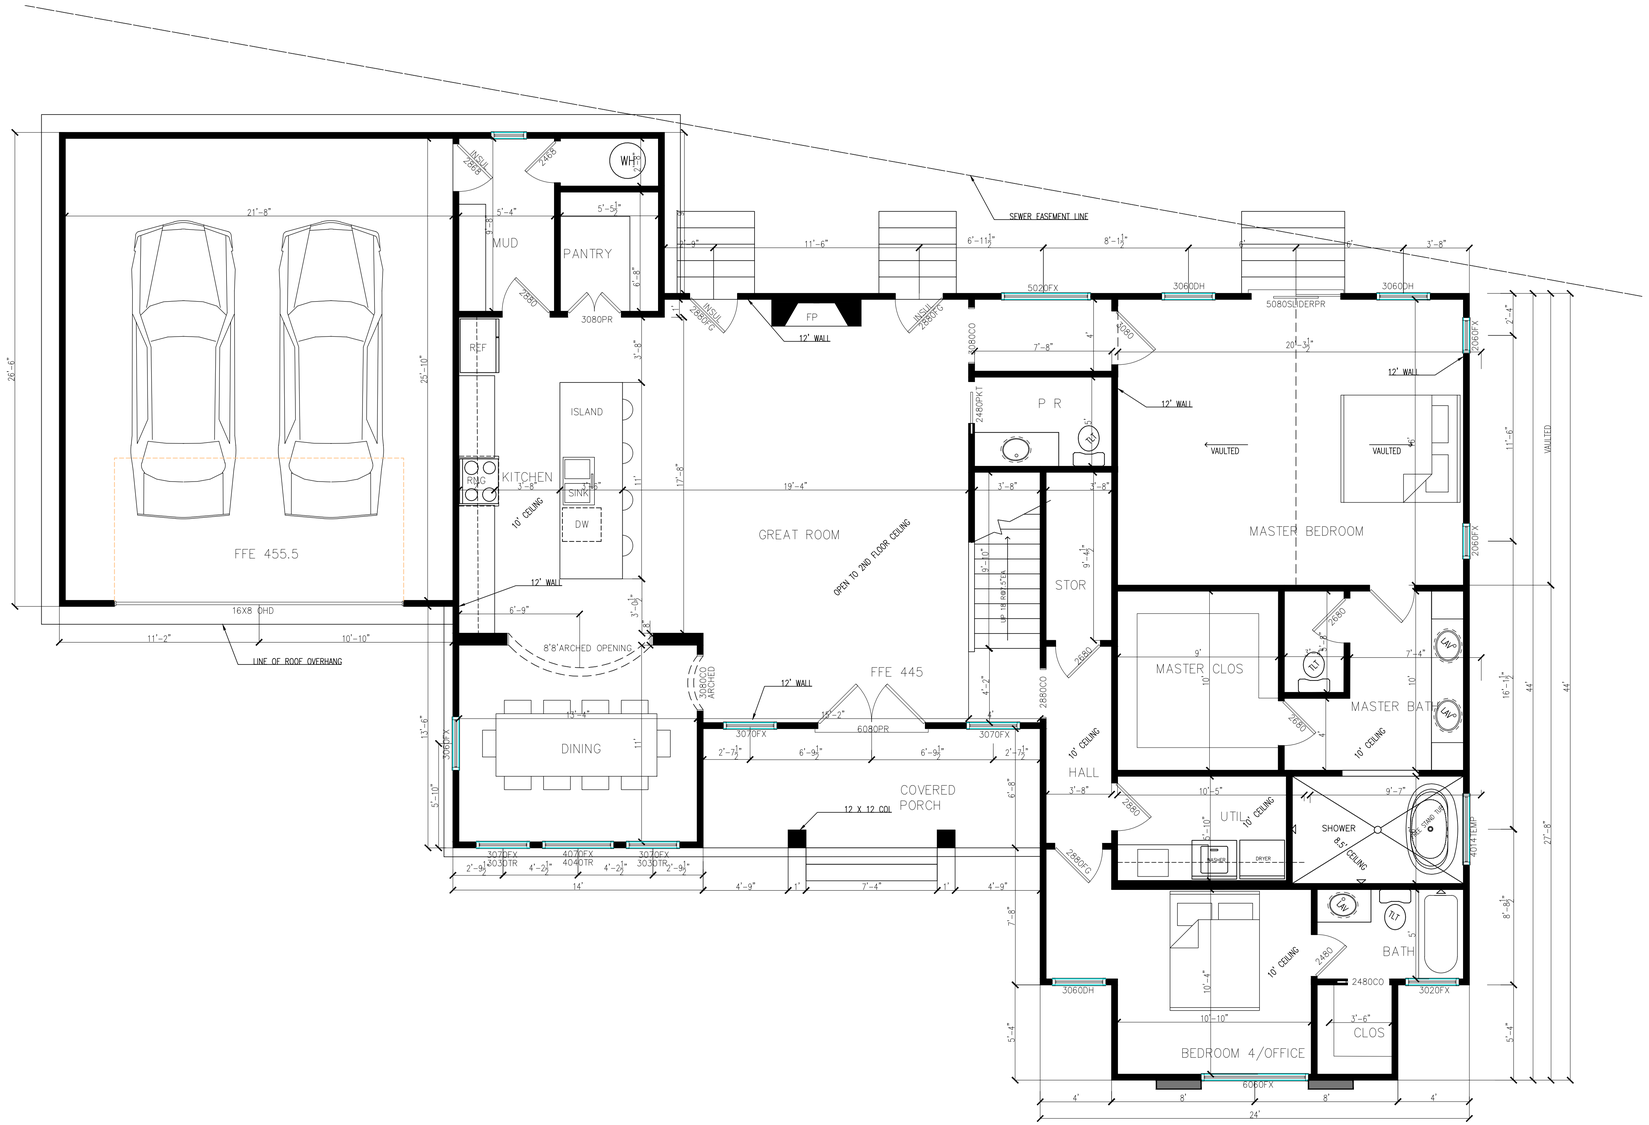

FIRST FLOOR PLAN

3/8" = 1'-0"

Area Schedule	
Level	Gross Area
Ist Floor	2,011 SF
2nd Floor	715 SF
Grand Total	2,726 SF
Garage	583 SF
Front Porch	126 SF

MYATT ARCHITECTURE

REVISED ISSUE

NEW HOUSE PLANS:
1421B ROSEBANK AVENUE
NASHVILLE TN, 37216

REVISIONS	
DATE	DESCRIPTION
PROJECT NO.	
DATE	02/09/2026
DRAWN BY	J. MYATT RA
CHECKED BY	

A2.1

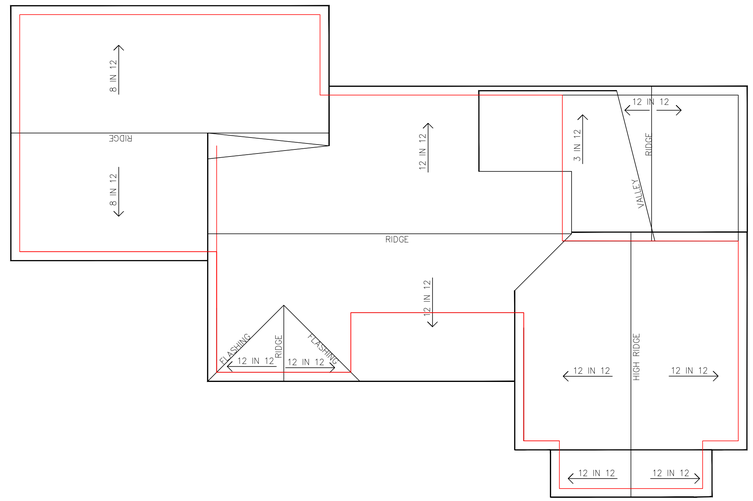

ROOF PLAN 1/8" = 1'-0"

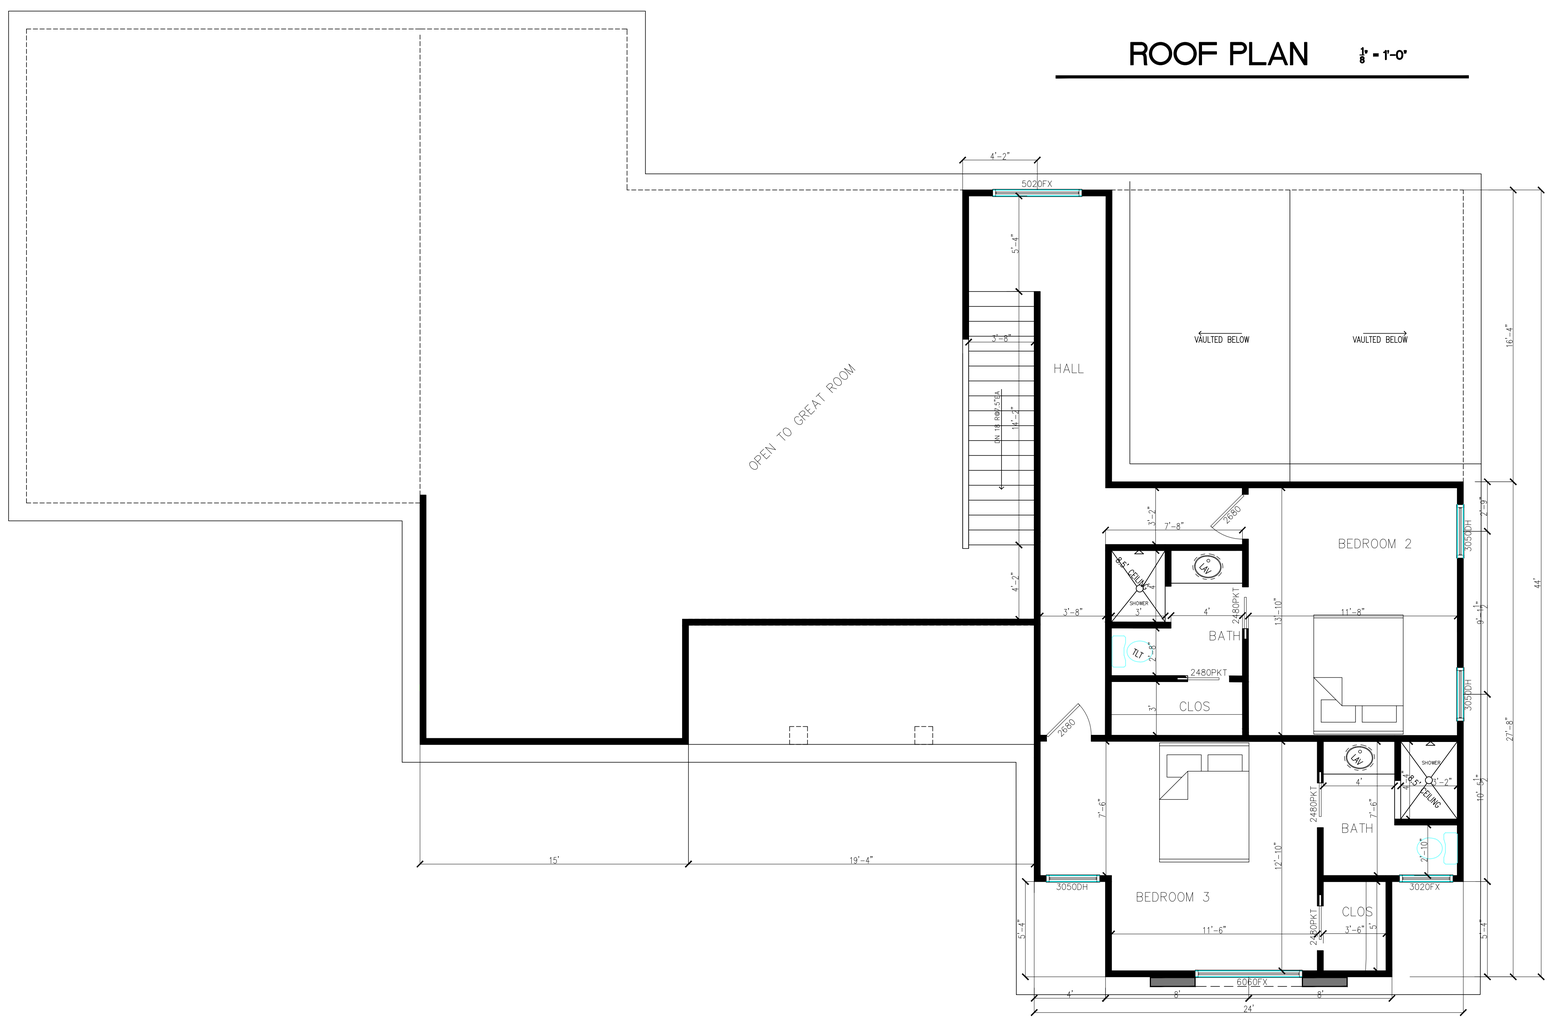

SECOND FLOOR PLAN 1/4" = 1'-0"

MYATT ARCHITECTURE

REVISED ISSUE

NEW HOUSE PLANS:
1421B ROSEBANK AVENUE
NASHVILLE TN, 37216

REVISIONS	
DATE	DESCRIPTION

PROJECT NO.	
DATE	02/09/2026
DRAWN BY	J. MYATT RA
CHECKED BY	

A2.2

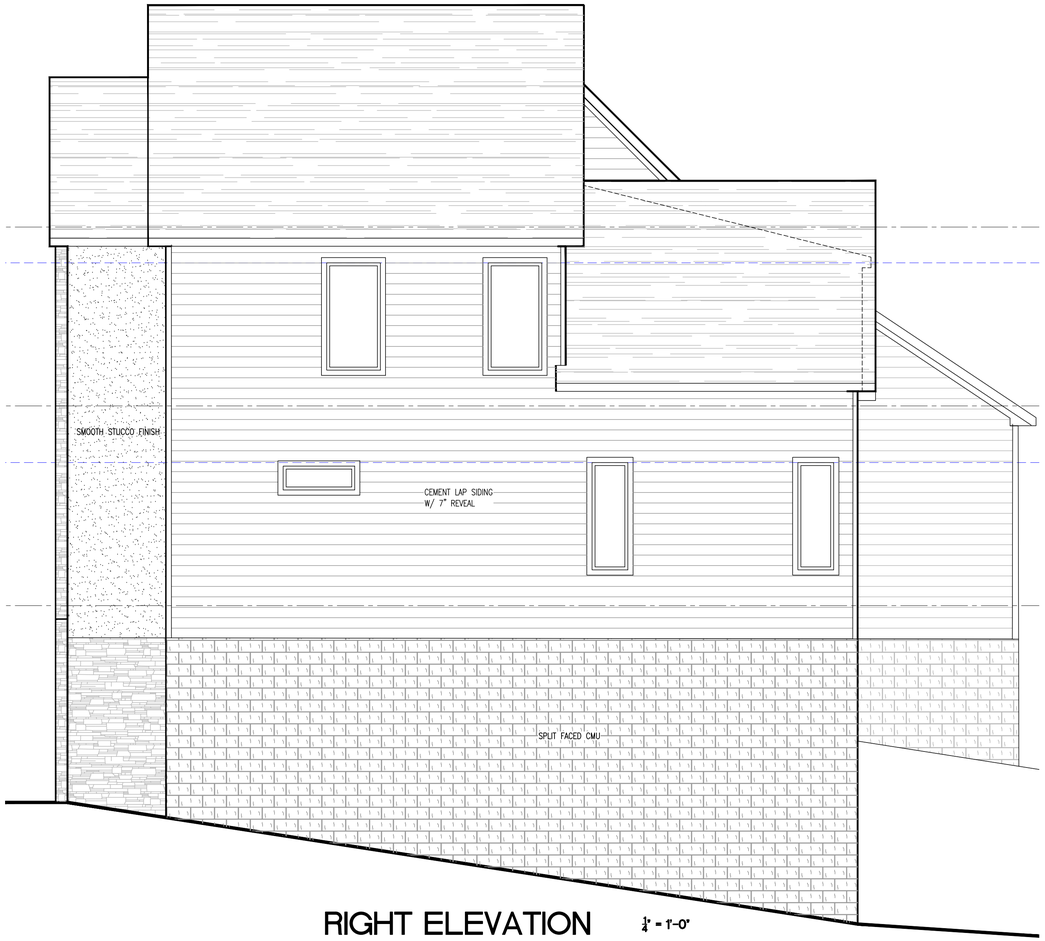

RIGHT ELEVATION ¼" = 1'-0"

FRONT ELEVATION ¼" = 1'-0"

FACING FRONT HOUSE

MYATT ARCHITECTURE

REVISED ISSUE

NEW HOUSE PLANS:
1421B ROSEBANK AVENUE
NASHVILLE TN, 37216

REVISIONS	
DATE	DESCRIPTION

PROJECT NO.	
DATE	02/09/2026
DRAWN BY	J. MYATT RA
CHECKED BY	

A3.1

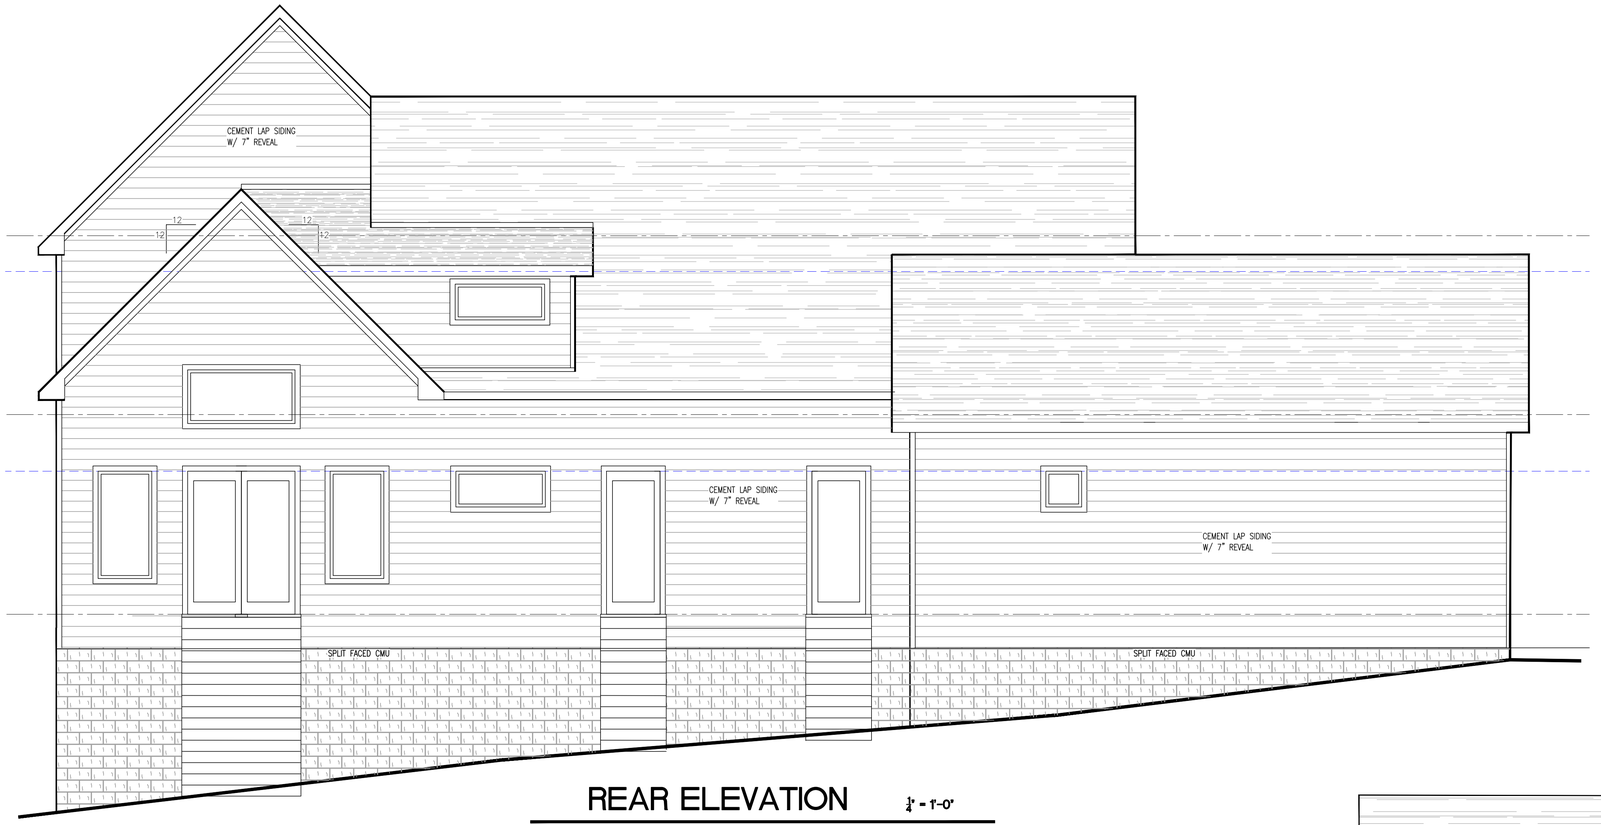

REAR ELEVATION $\frac{1}{4}$" = 1'-0"

LEFT ELEVATION $\frac{1}{4}$" = 1'-0"

MYATT ARCHITECTURE

REVISED ISSUE

NEW HOUSE PLANS:
1421B ROSEBANK AVENUE
NASHVILLE TN, 37216

REVISIONS	
DATE	DESCRIPTION
PROJECT NO.	
DATE	02/09/2026
DRAWN BY	J. MYATT RA
CHECKED BY	

A3.2